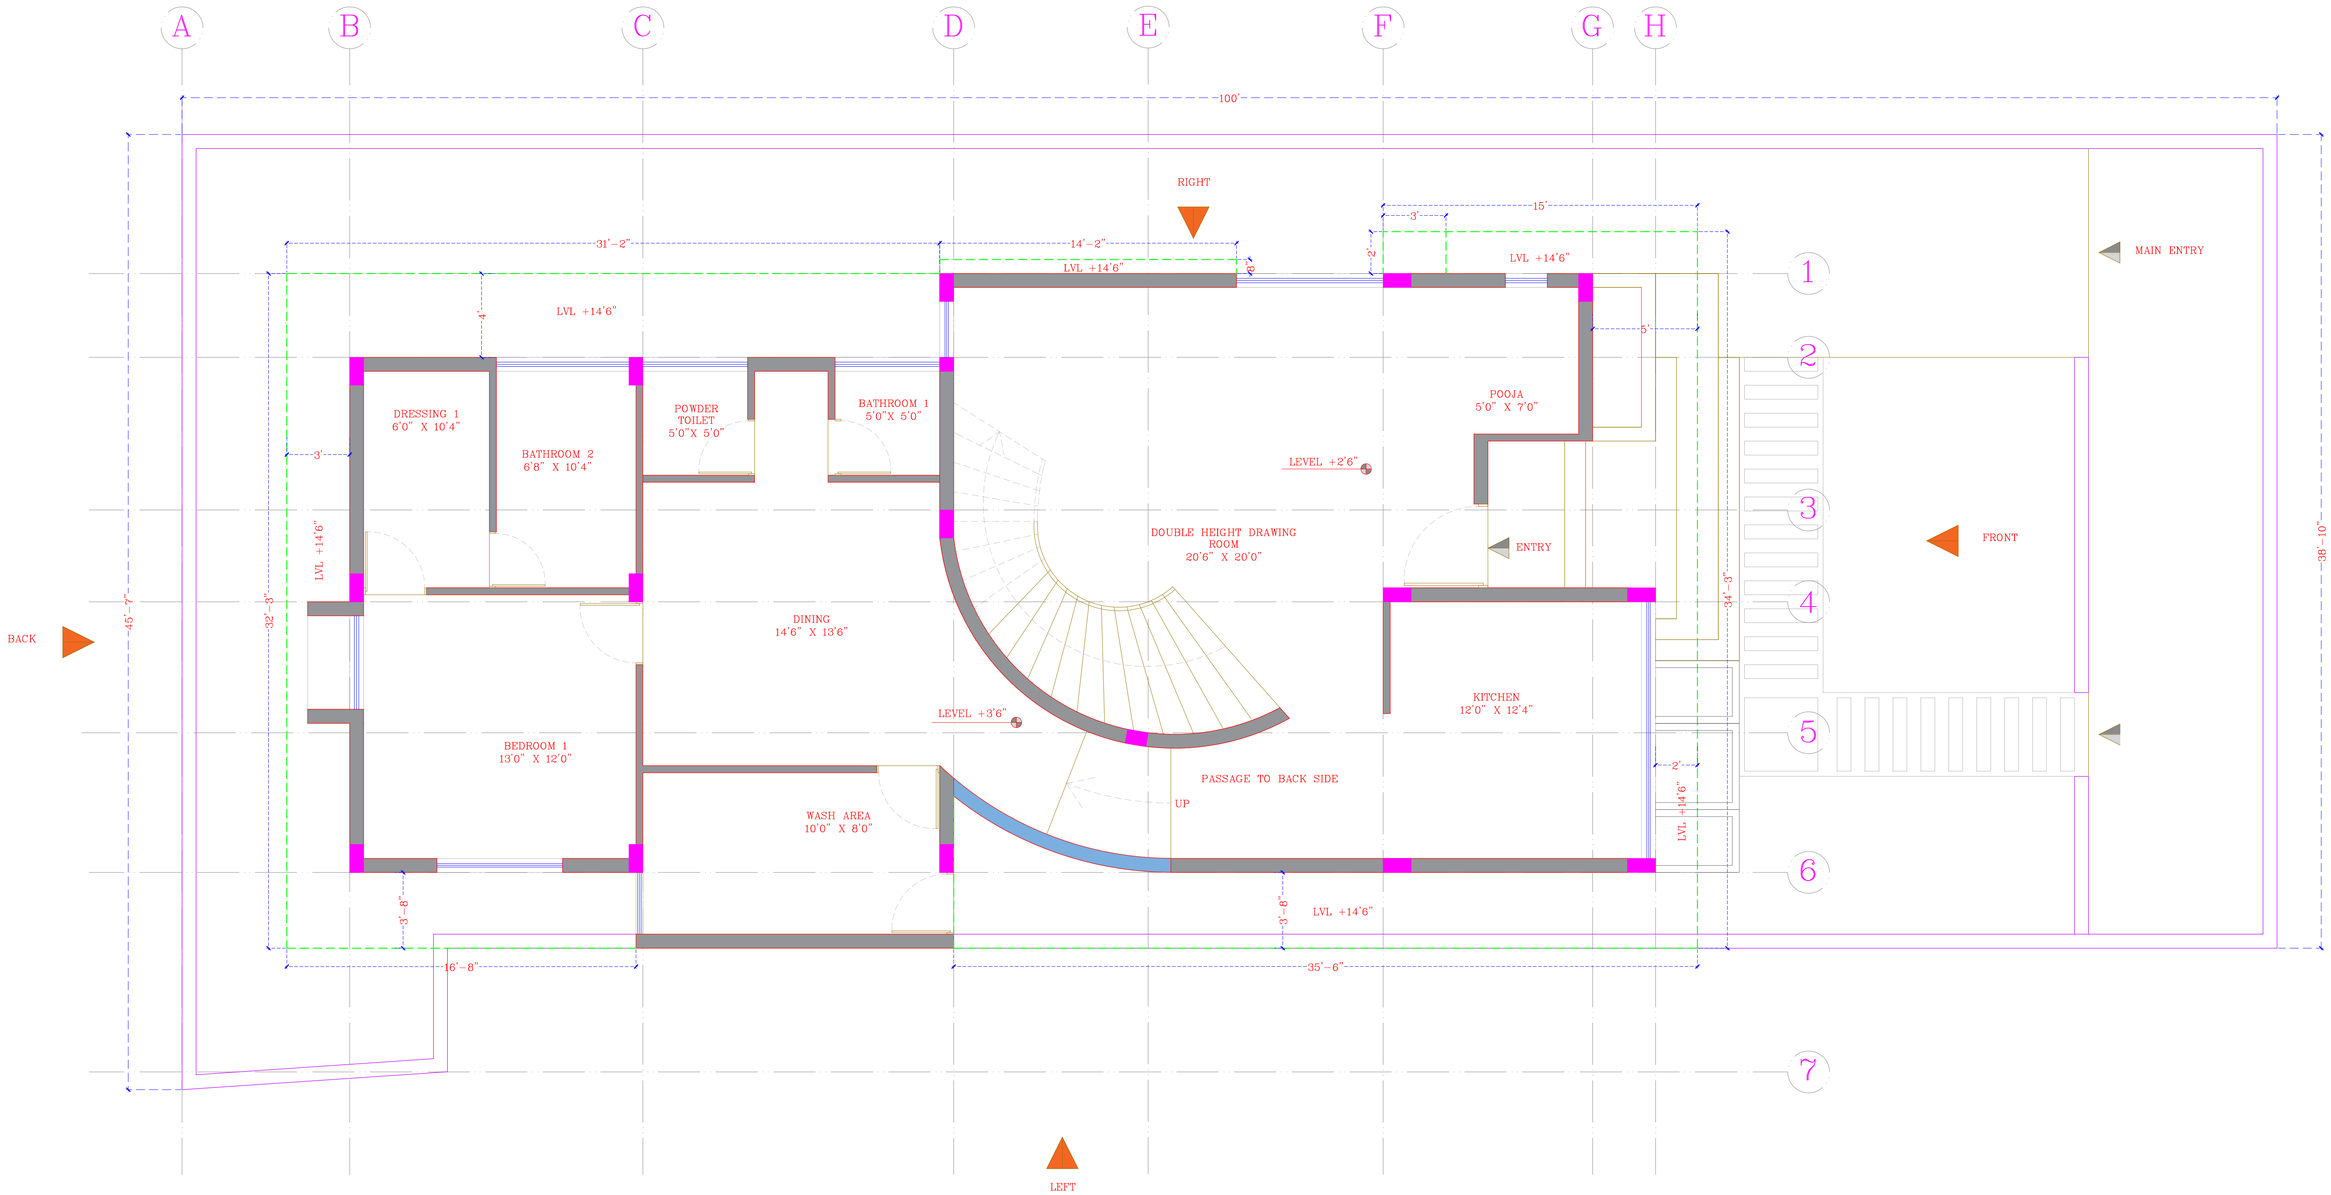

GROUND FLOOR ELEVATION MARKING PLAN

PROPOSED LAYOUT FOR
MR.SANJAY JI

DESIGNED BY: AR. EKTA MISHRA

A4 A R C H I T E C T

NORTH

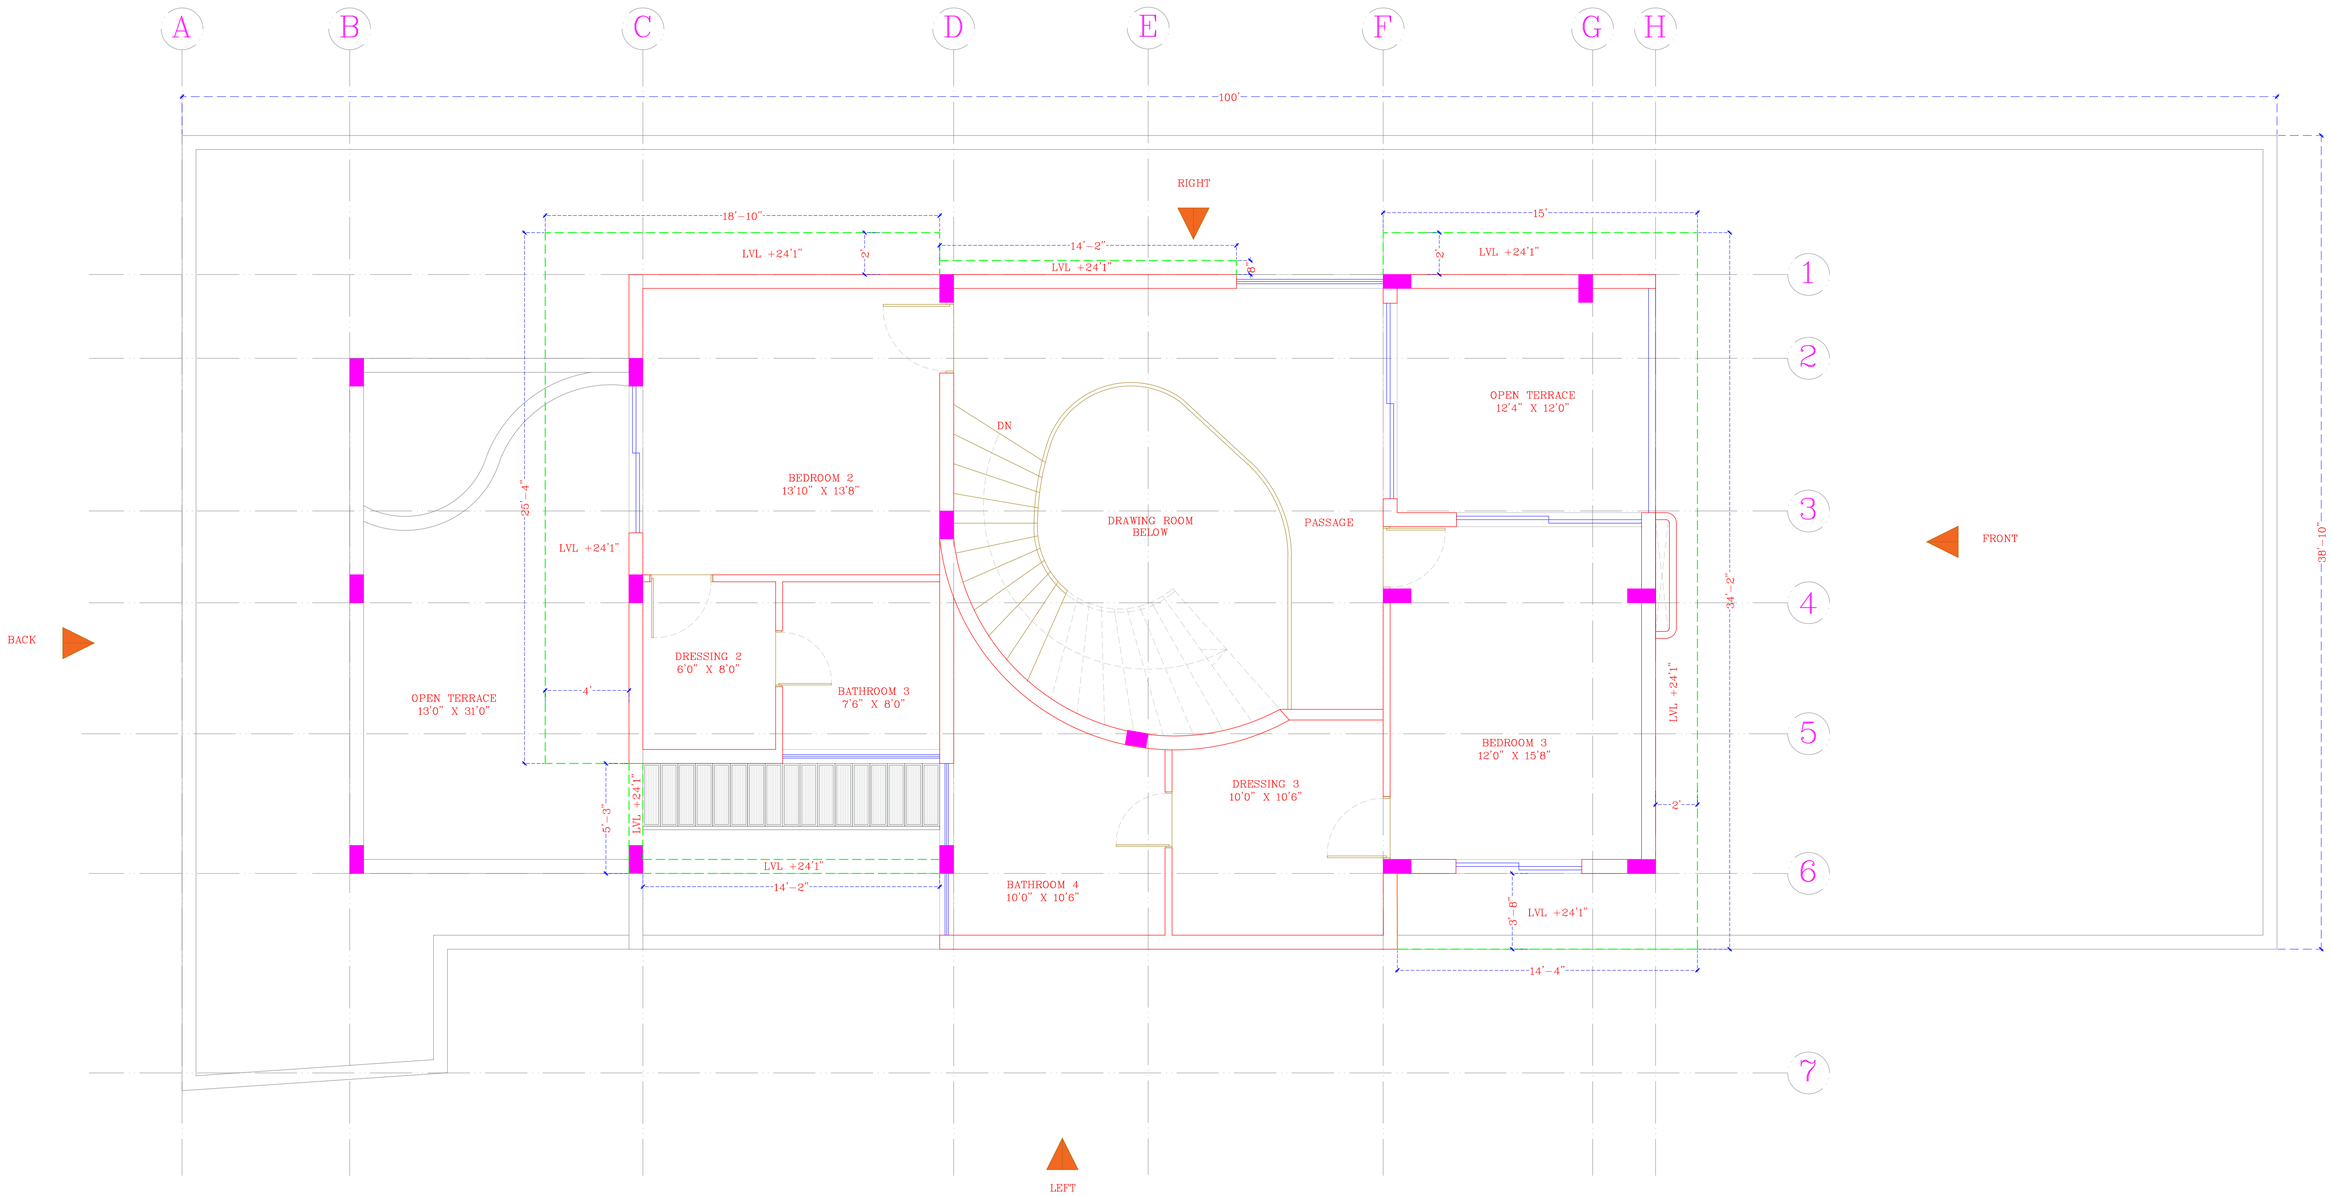

FIRST FLOOR ELEVATION MARKING PLAN

PROPOSED LAYOUT FOR
MR.SANJAY JI

DESIGNED BY: AR. EKTA MISHRA

A4 A R C H I T E C T

NORTH

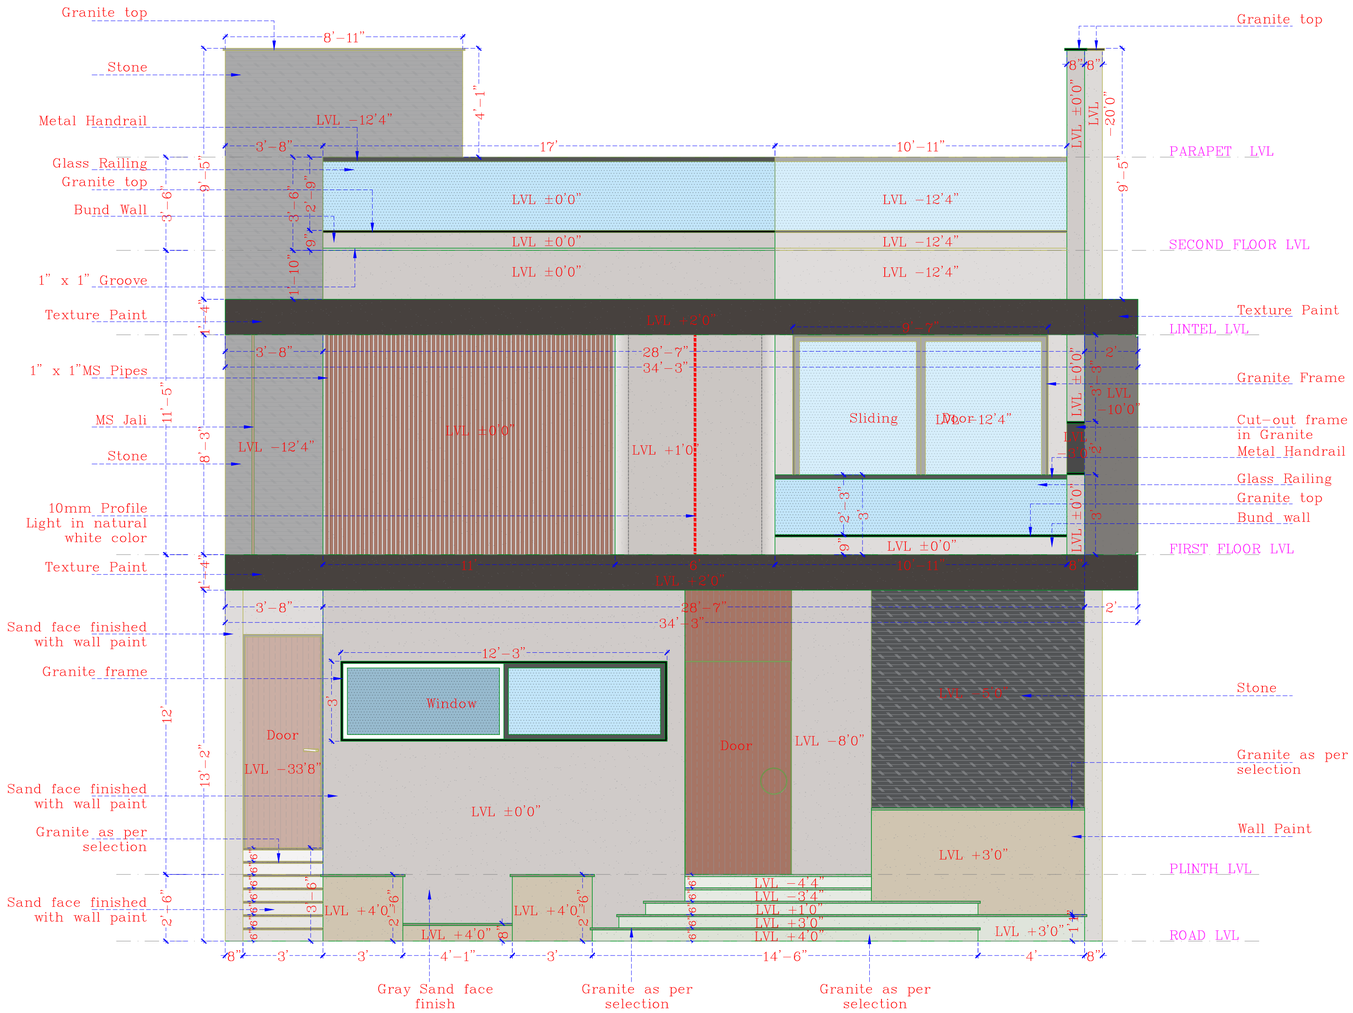

FRONT ELEVATION

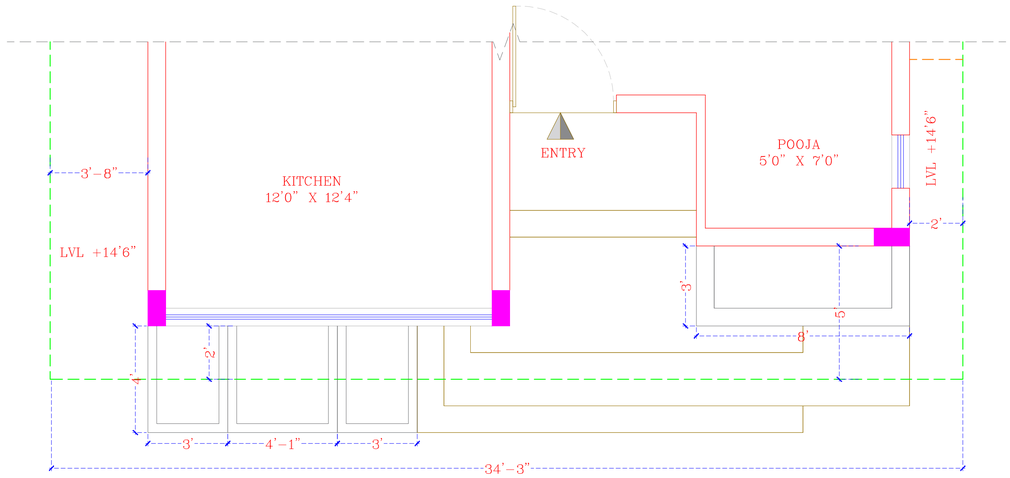

GROUND FLOOR PART PLAN

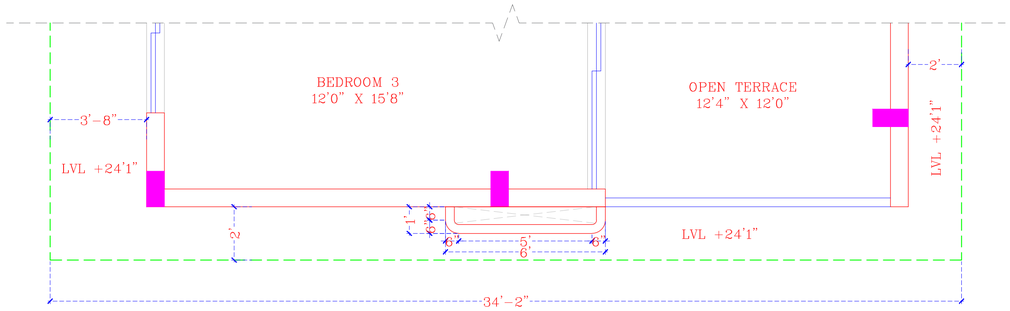

FIRST FLOOR PART PLAN

FRONT ELEVATION DETAIL

PROPOSED ELEVATION FOR
MR.SANJAY JI

DESIGNED BY: AR. EKTA MISHRA

A4 A R C H I T E C T

NORTH

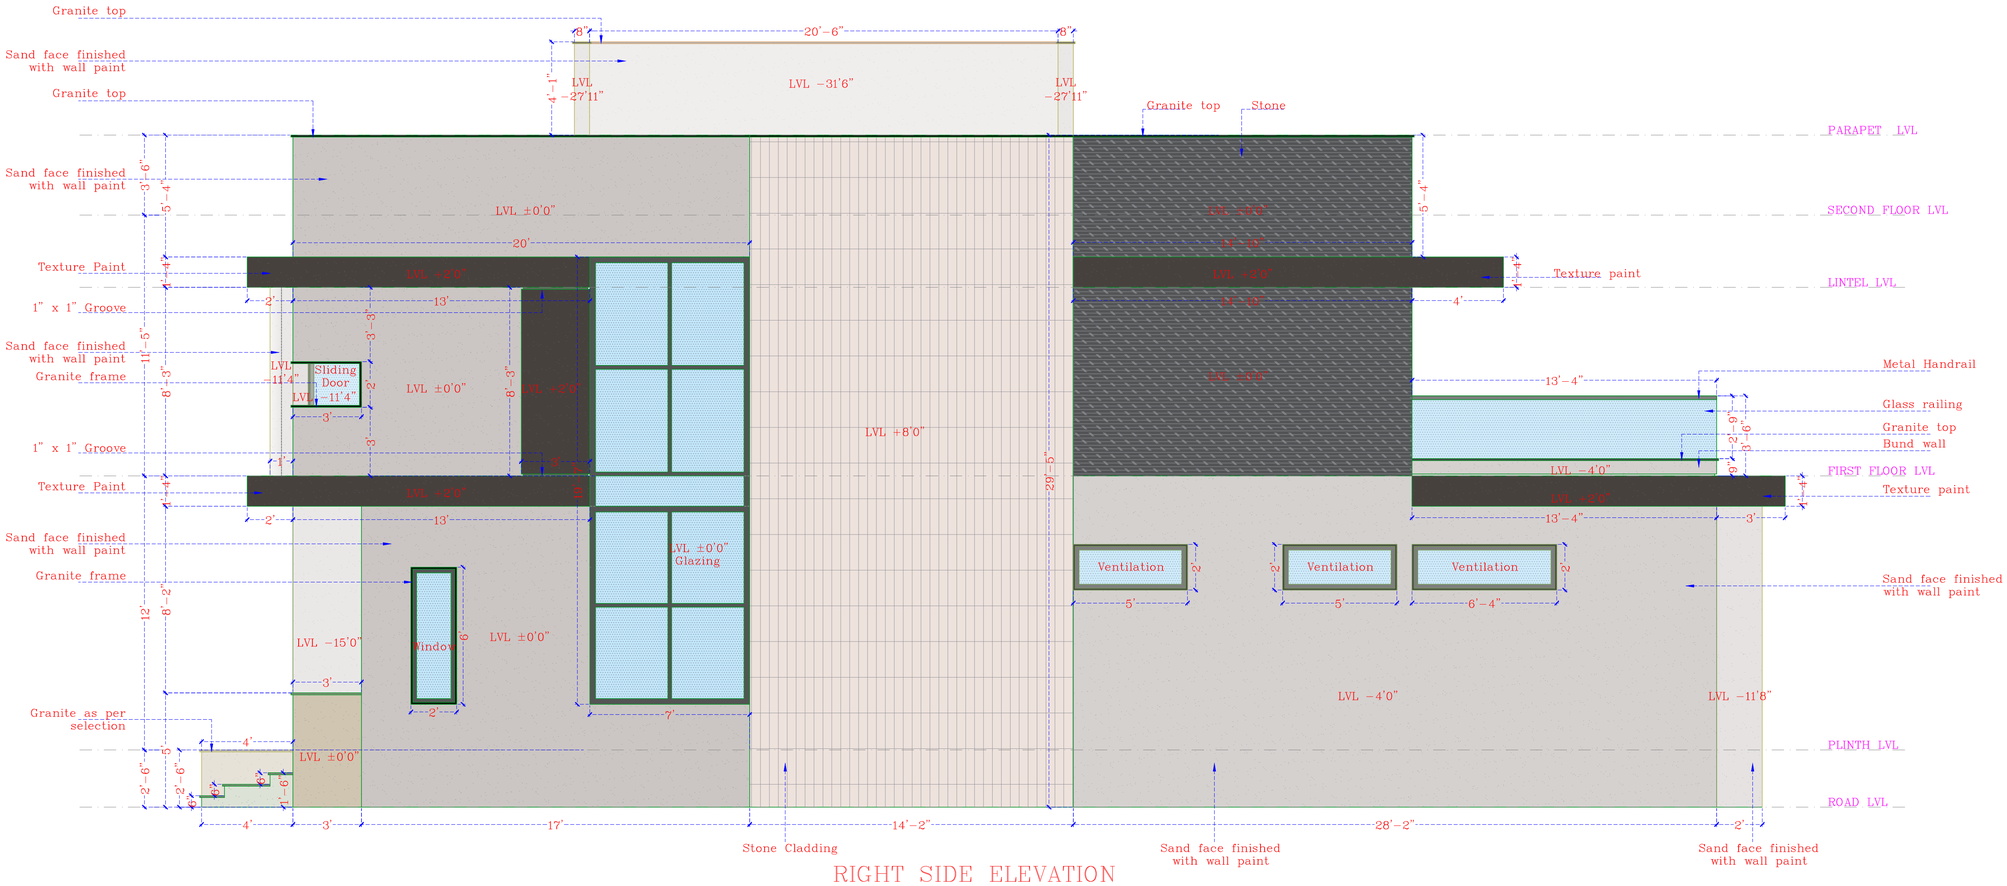

RIGHT SIDE ELEVATION

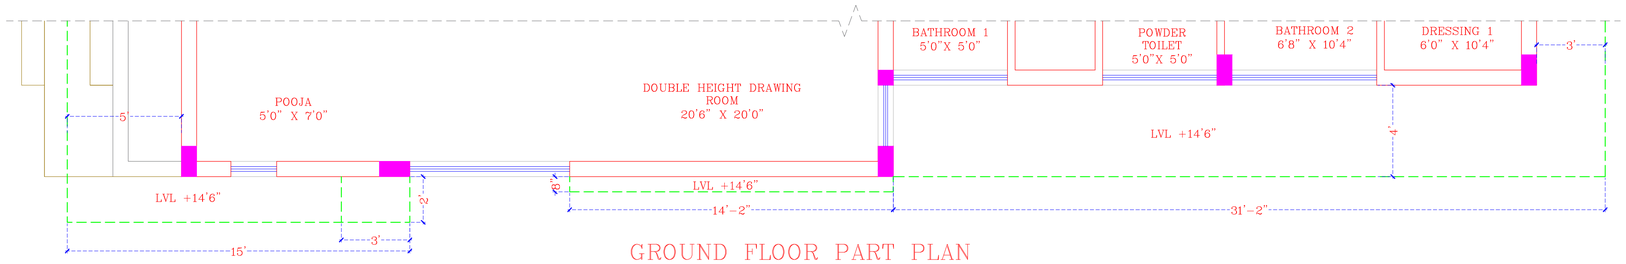

GROUND FLOOR PART PLAN

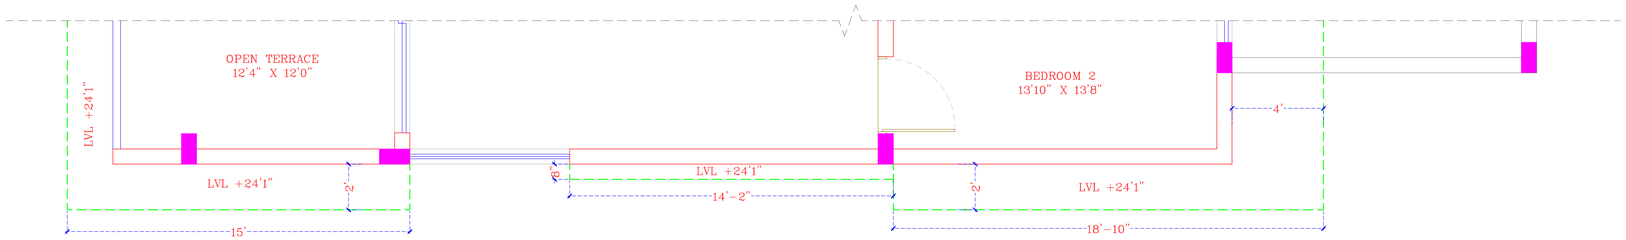

FIRST FLOOR PART PLAN

RIGHT SIDE ELEVATION DETAIL

PROPOSED ELEVATION FOR MR.SANJAY JI

DESIGNED BY: AR. EKTA MISHRA

A4 A R C H I T E C T

NORTH

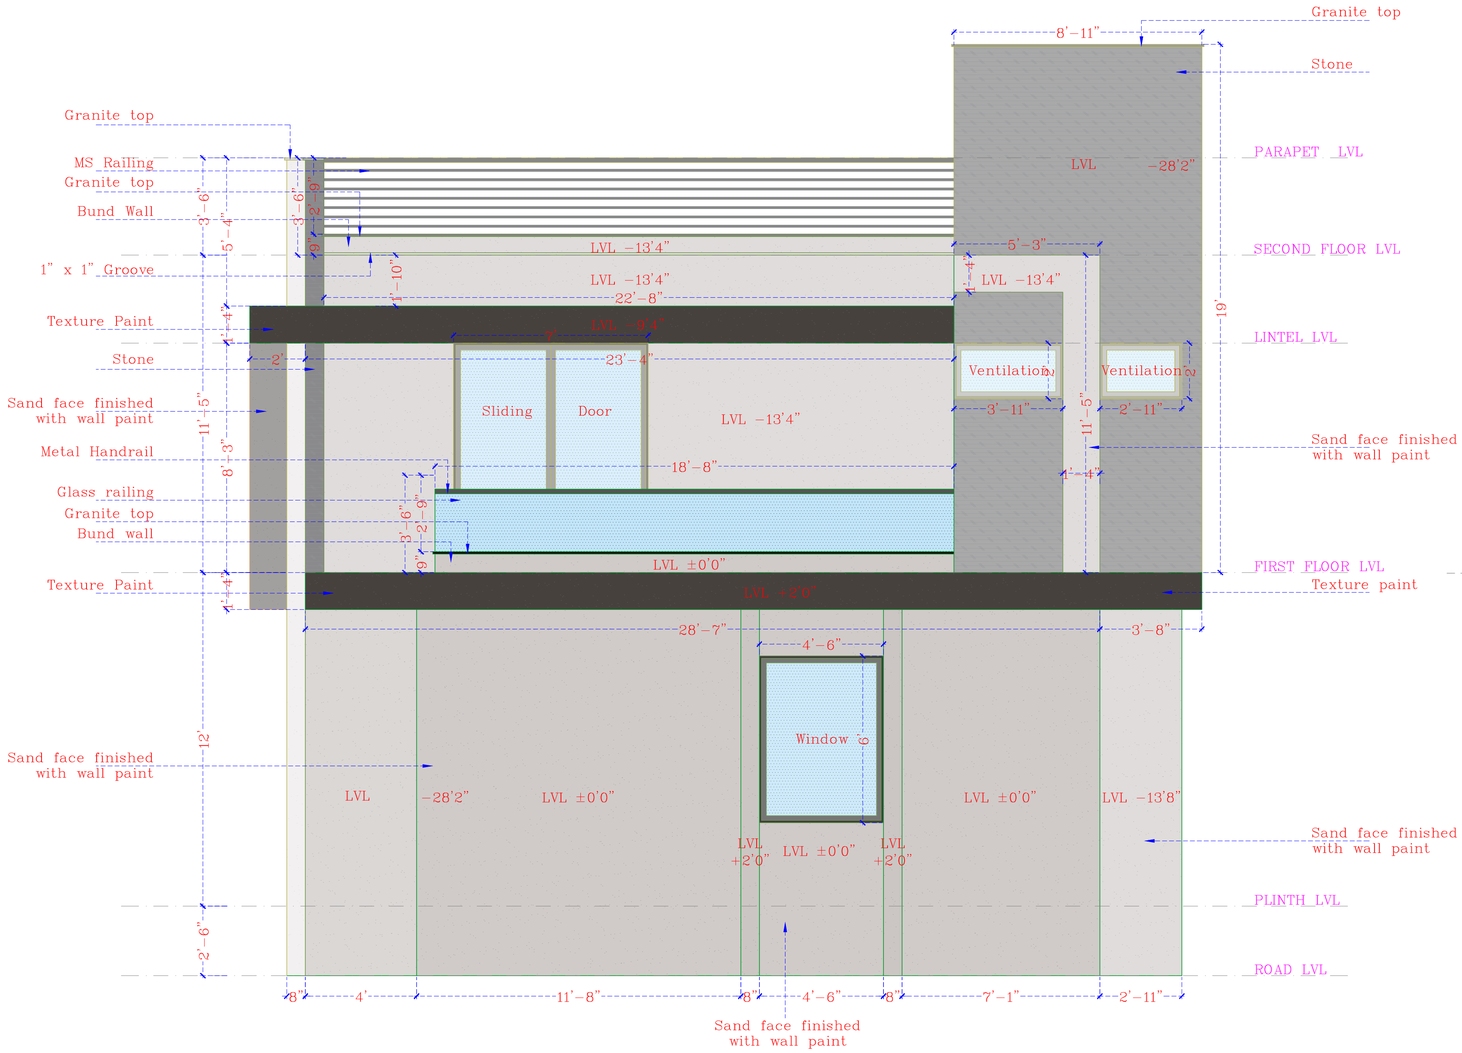

BACK ELEVATION

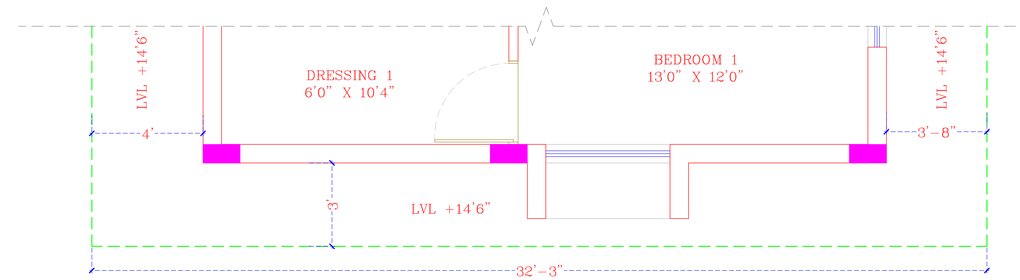

GROUND FLOOR PART PLAN

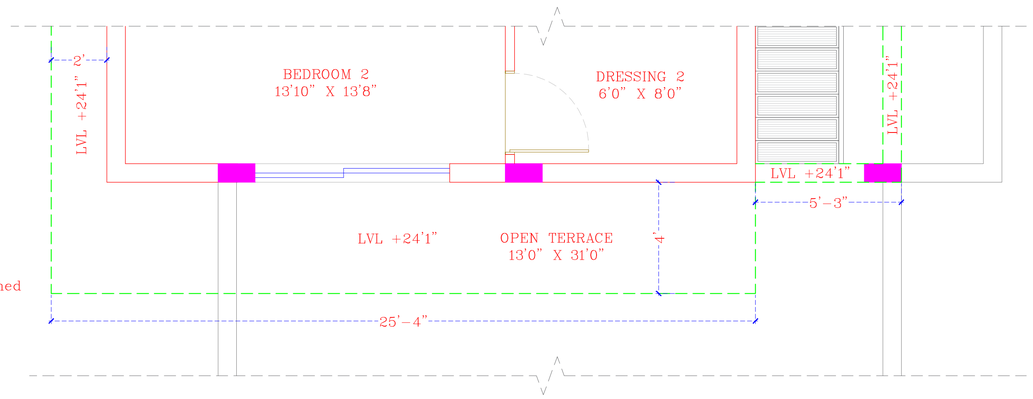

FIRST FLOOR PART PLAN

BACK ELEVATION DETAIL

PROPOSED ELEVATION FOR
MR.SANJAY JI

DESIGNED BY: AR. EKTA MISHRA

A4 A R C H I T E C T

NORTH

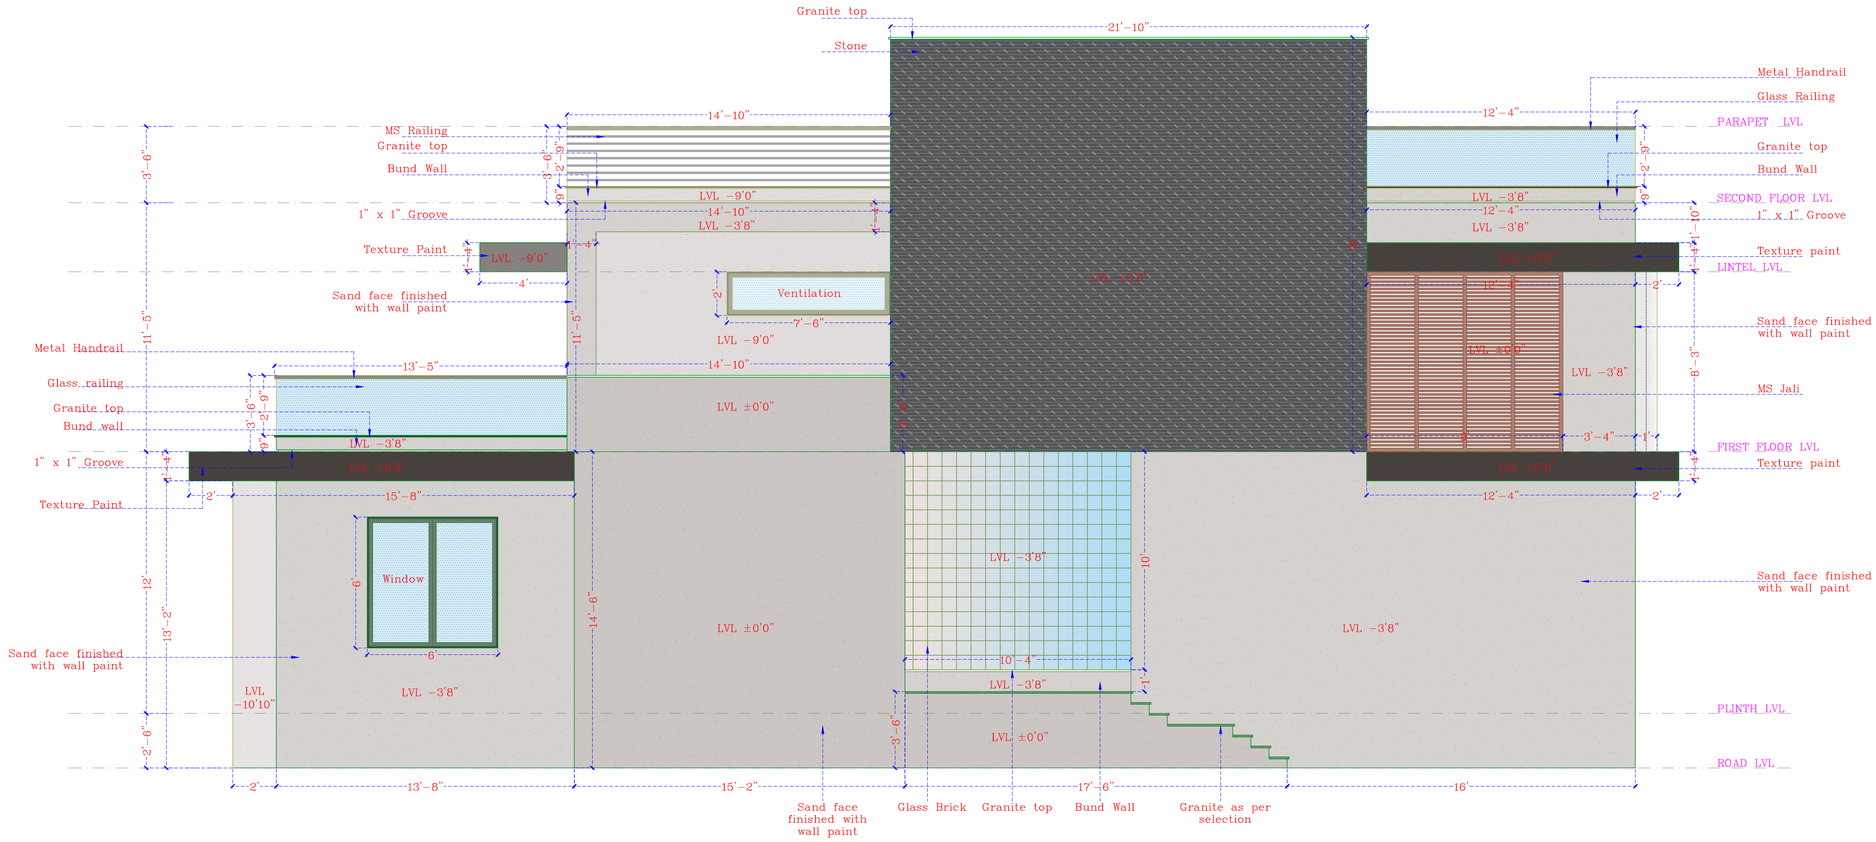

LEFT SIDE ELEVATION

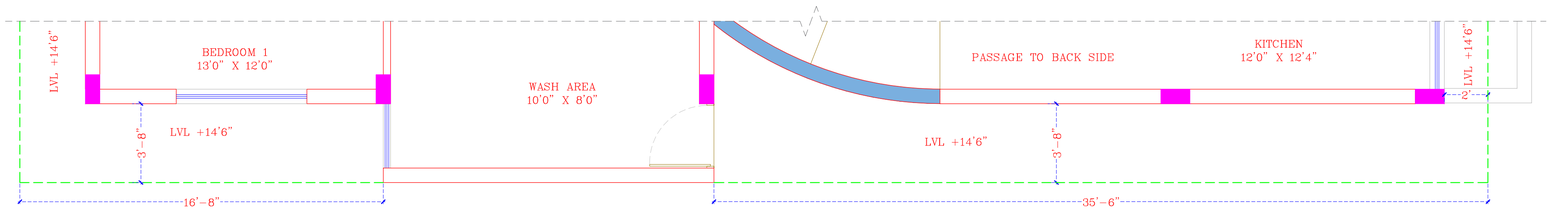

GROUND FLOOR PART PLAN

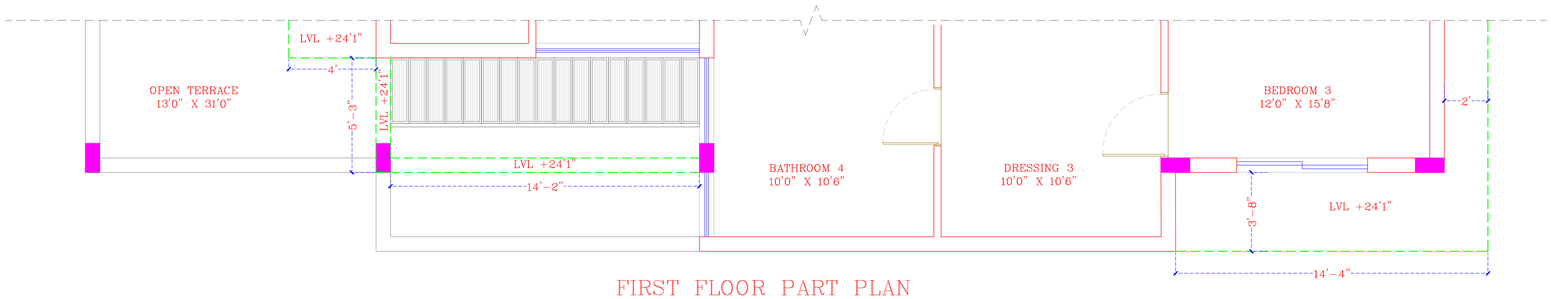

FIRST FLOOR PART PLAN

LEFT SIDE ELEVATION DETAIL

PROPOSED ELEVATION FOR MR.SANJAY JI

DESIGNED BY: AR. EKTA MISHRA

A4 A R C H I T E C T

NORTH