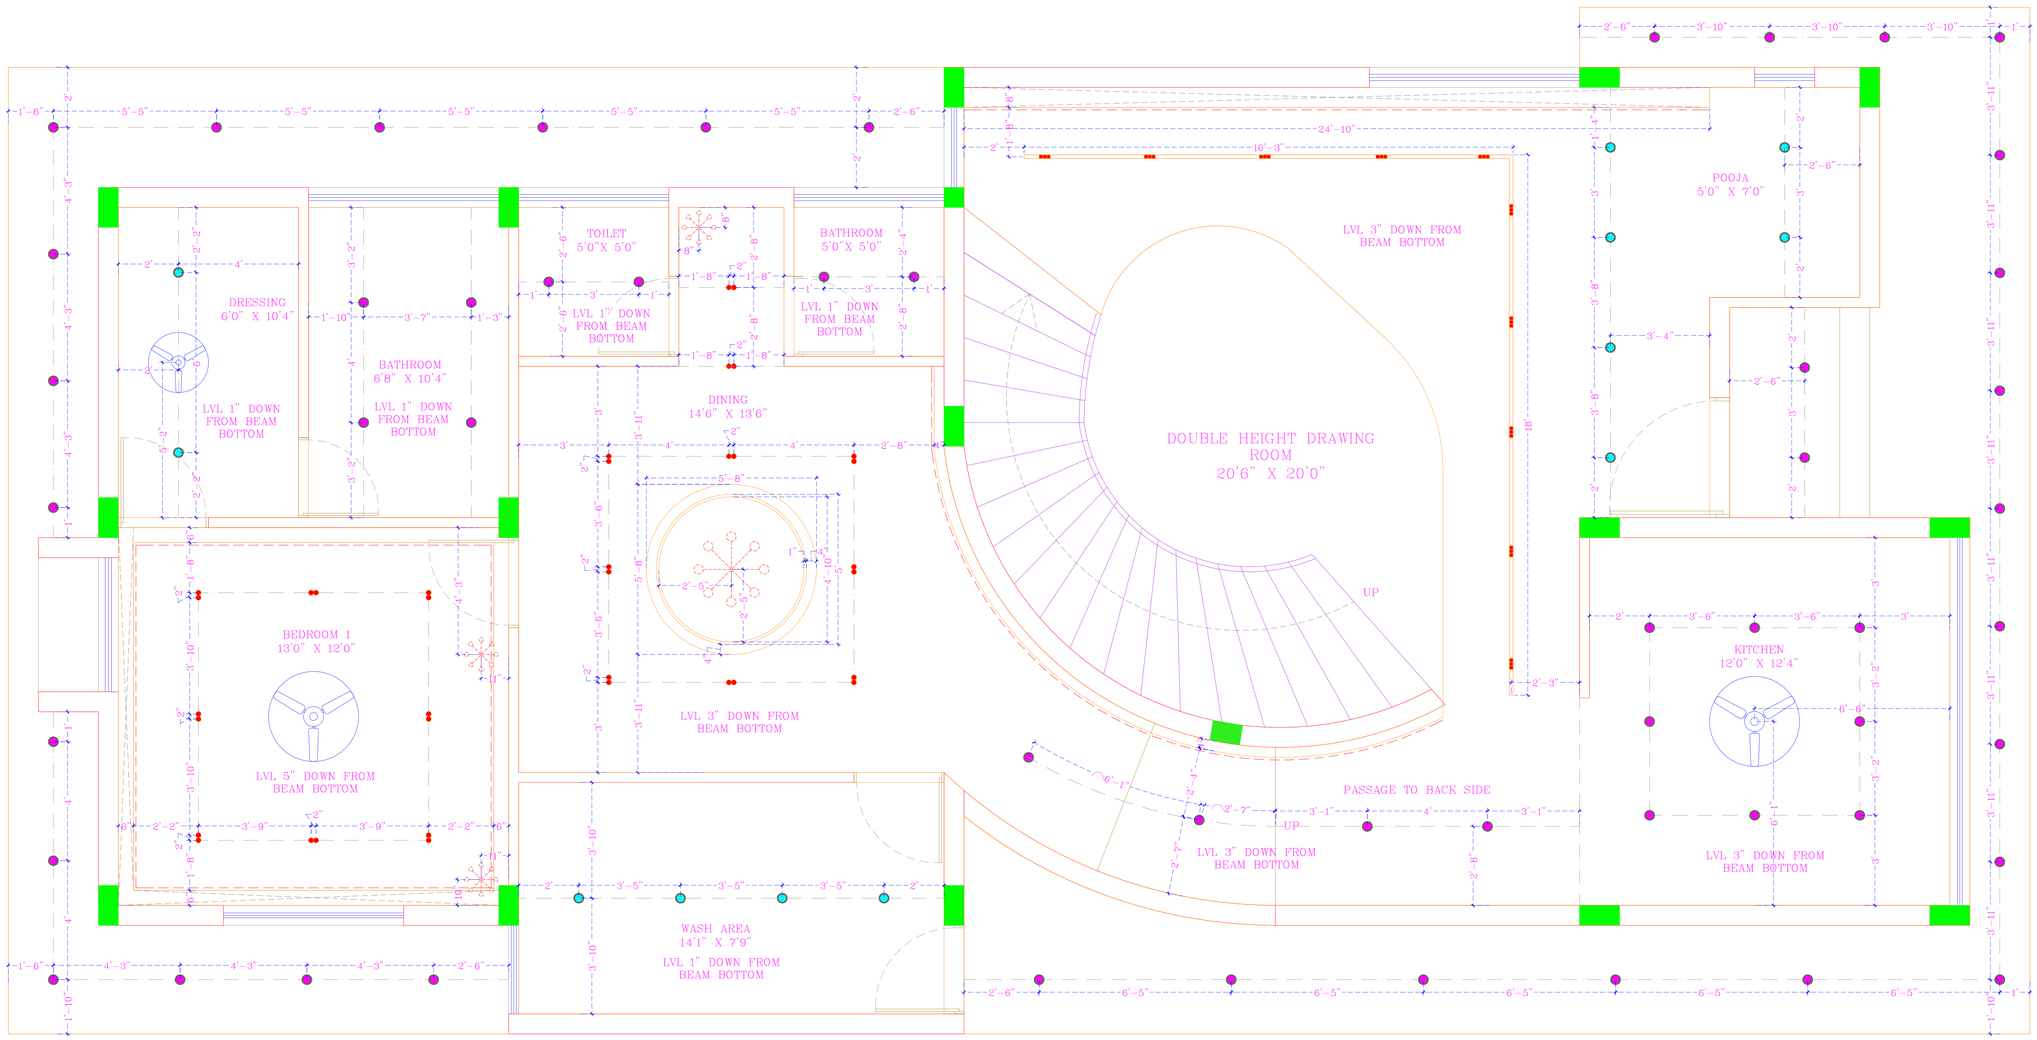


HANGING LIGHT

FOCUS LIGHT

PROFILE LIGHT

7W ADJUSTABLE COB LIGHT

COVE LIGHT

MAGNETIC TRACK LIGHT

CEILING FAN

12W ADJUSTABLE COB LIGHT

# GROUND FLOOR FALSE CEILING LAYOUT

PROPOSED LAYOUT FOR
MR.SANJAY JI

DESIGNED BY: AR. EKTA MISHRA

A4 A R C H I T E C T

NORTH

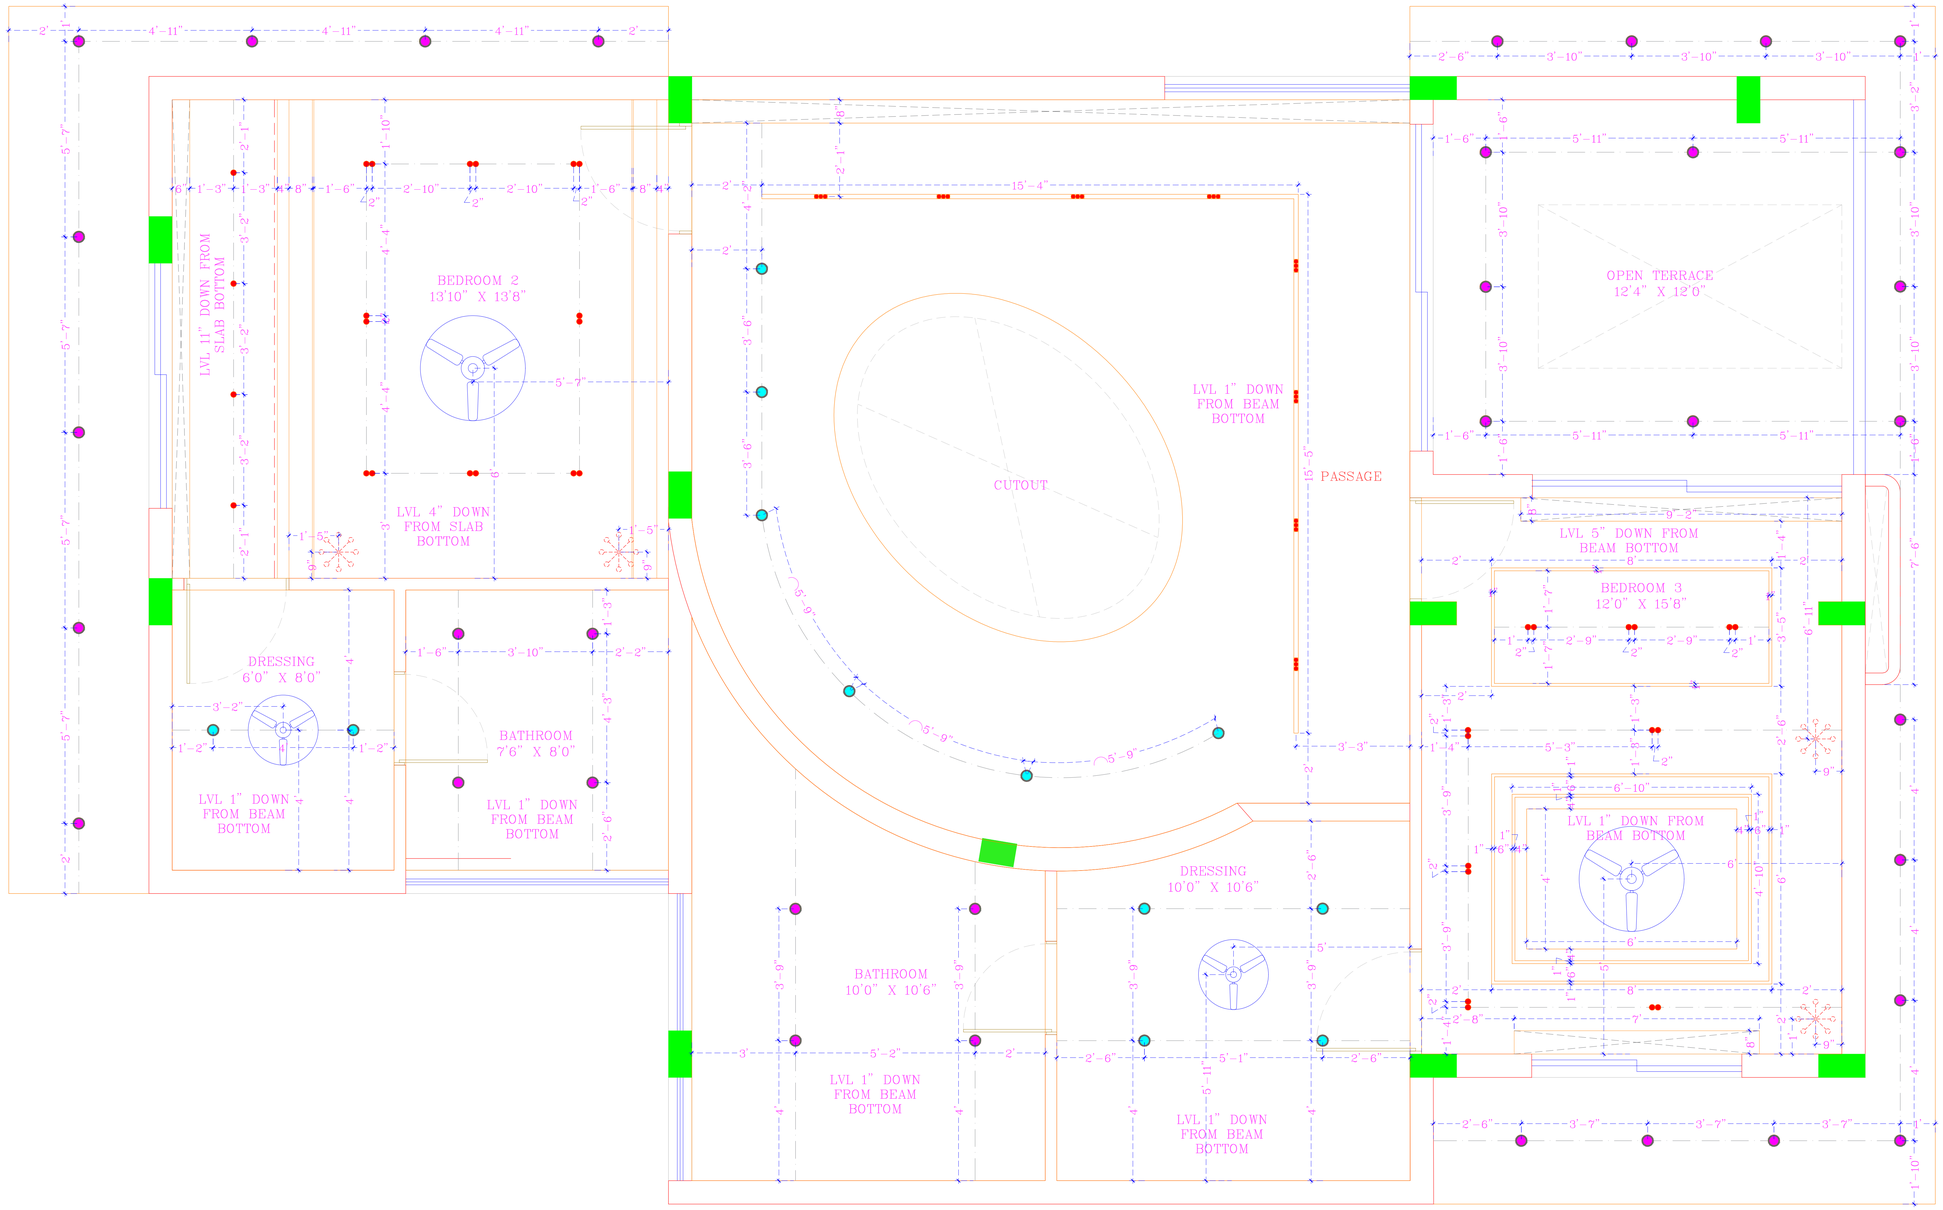


HANGING LIGHT

FOCUS LIGHT

PROFILE LIGHT

7W ADJUSTABLE COB LIGHT

COVE LIGHT

MAGNETIC TRACK LIGHT

CEILING FAN

12W ADJUSTABLE COB LIGHT

# FIRST FLOOR FALSE CEILING LAYOUT

PROPOSED LAYOUT FOR MR.SANJAY JI

DESIGNED BY: AR. EKTA MISHRA

A4 A R C H I T E C T

NORTH

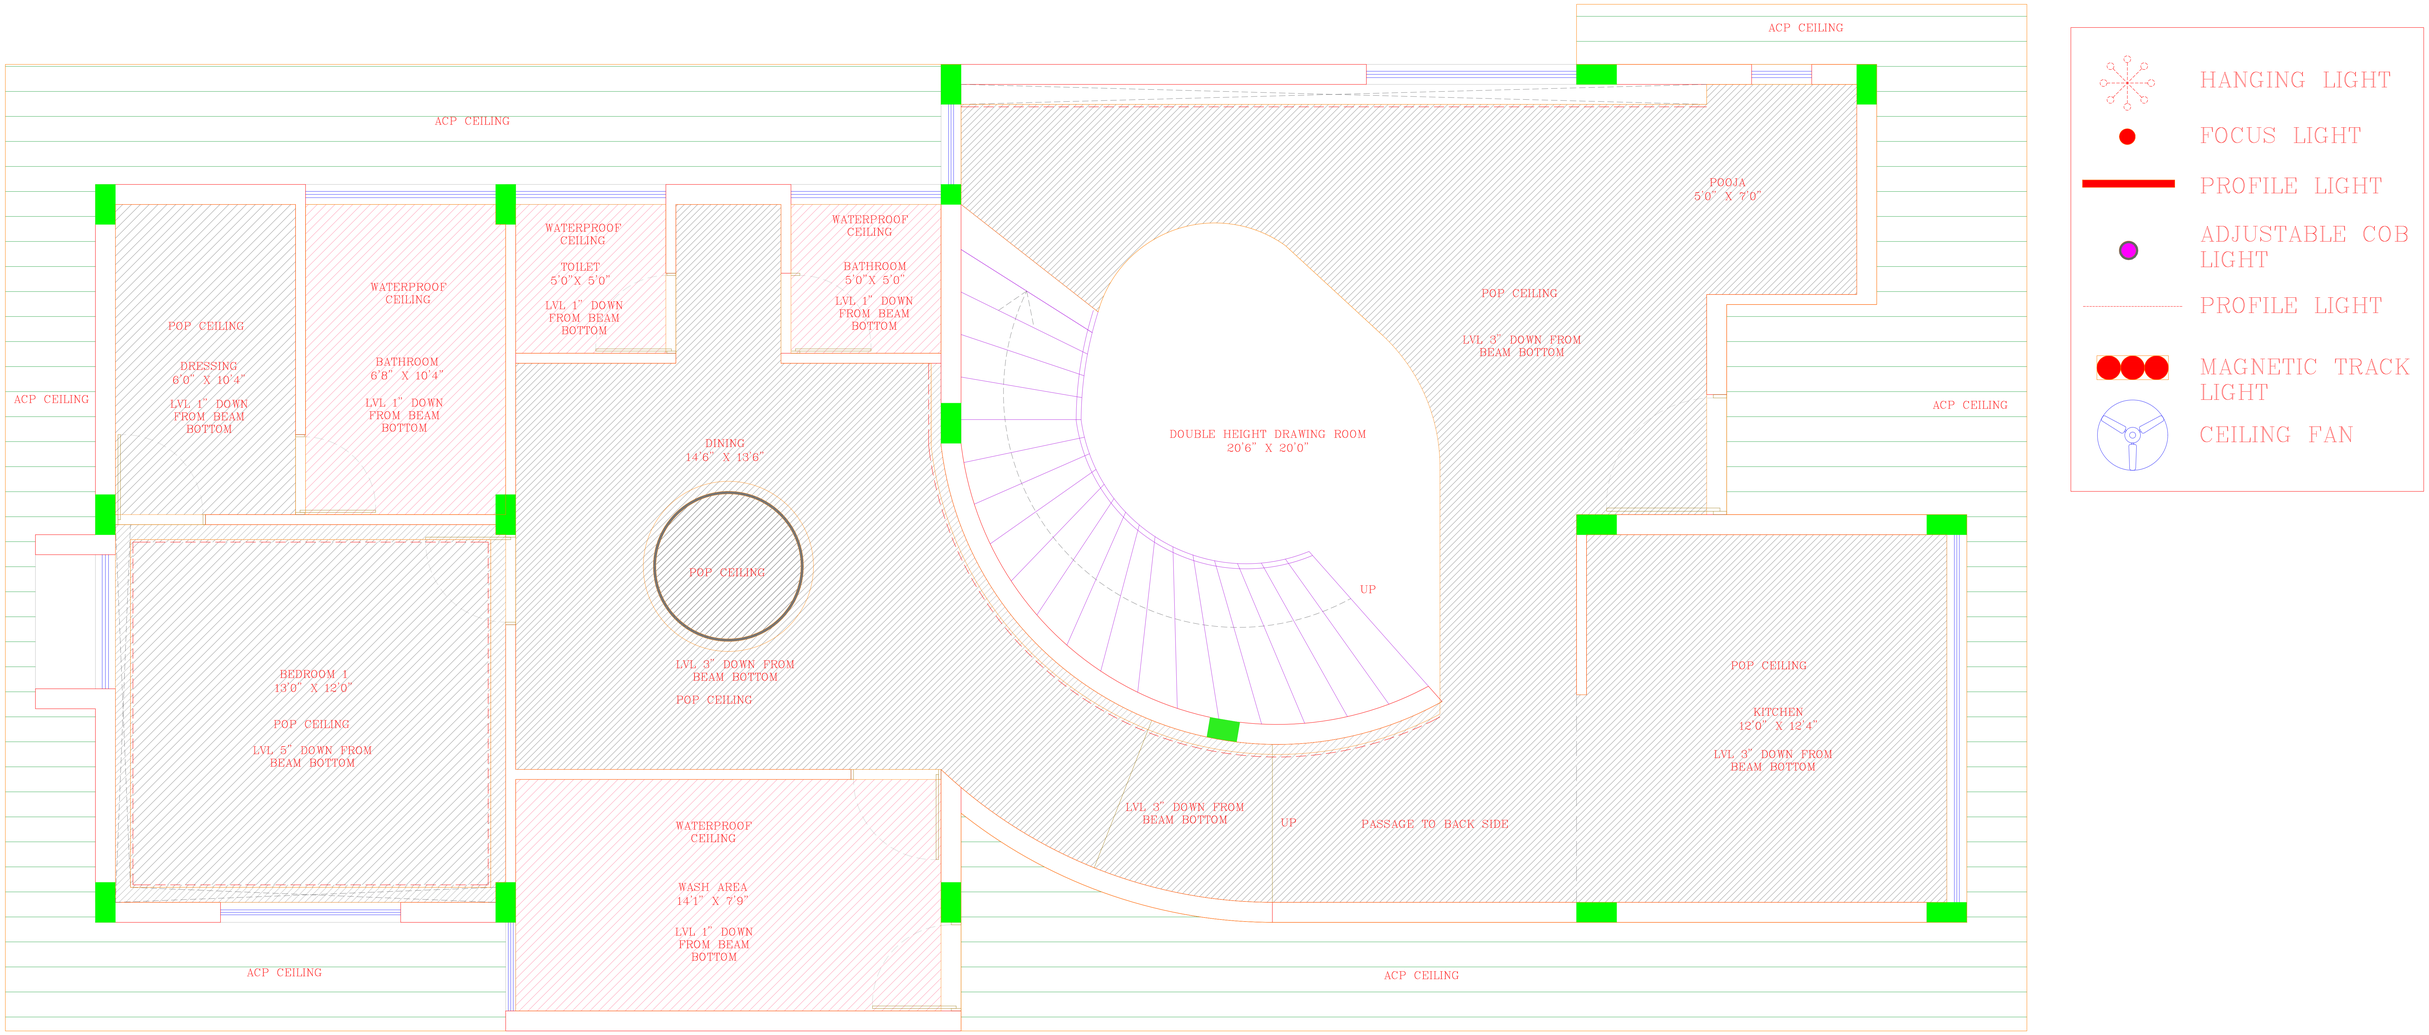


# GROUND FLOOR FALSE CEILING LAYOUT

PROPOSED LAYOUT FOR
MR.SANJAY JI

DESIGNED BY: AR. EKTA MISHRA

A4 A R C H I T E C T

NORTH

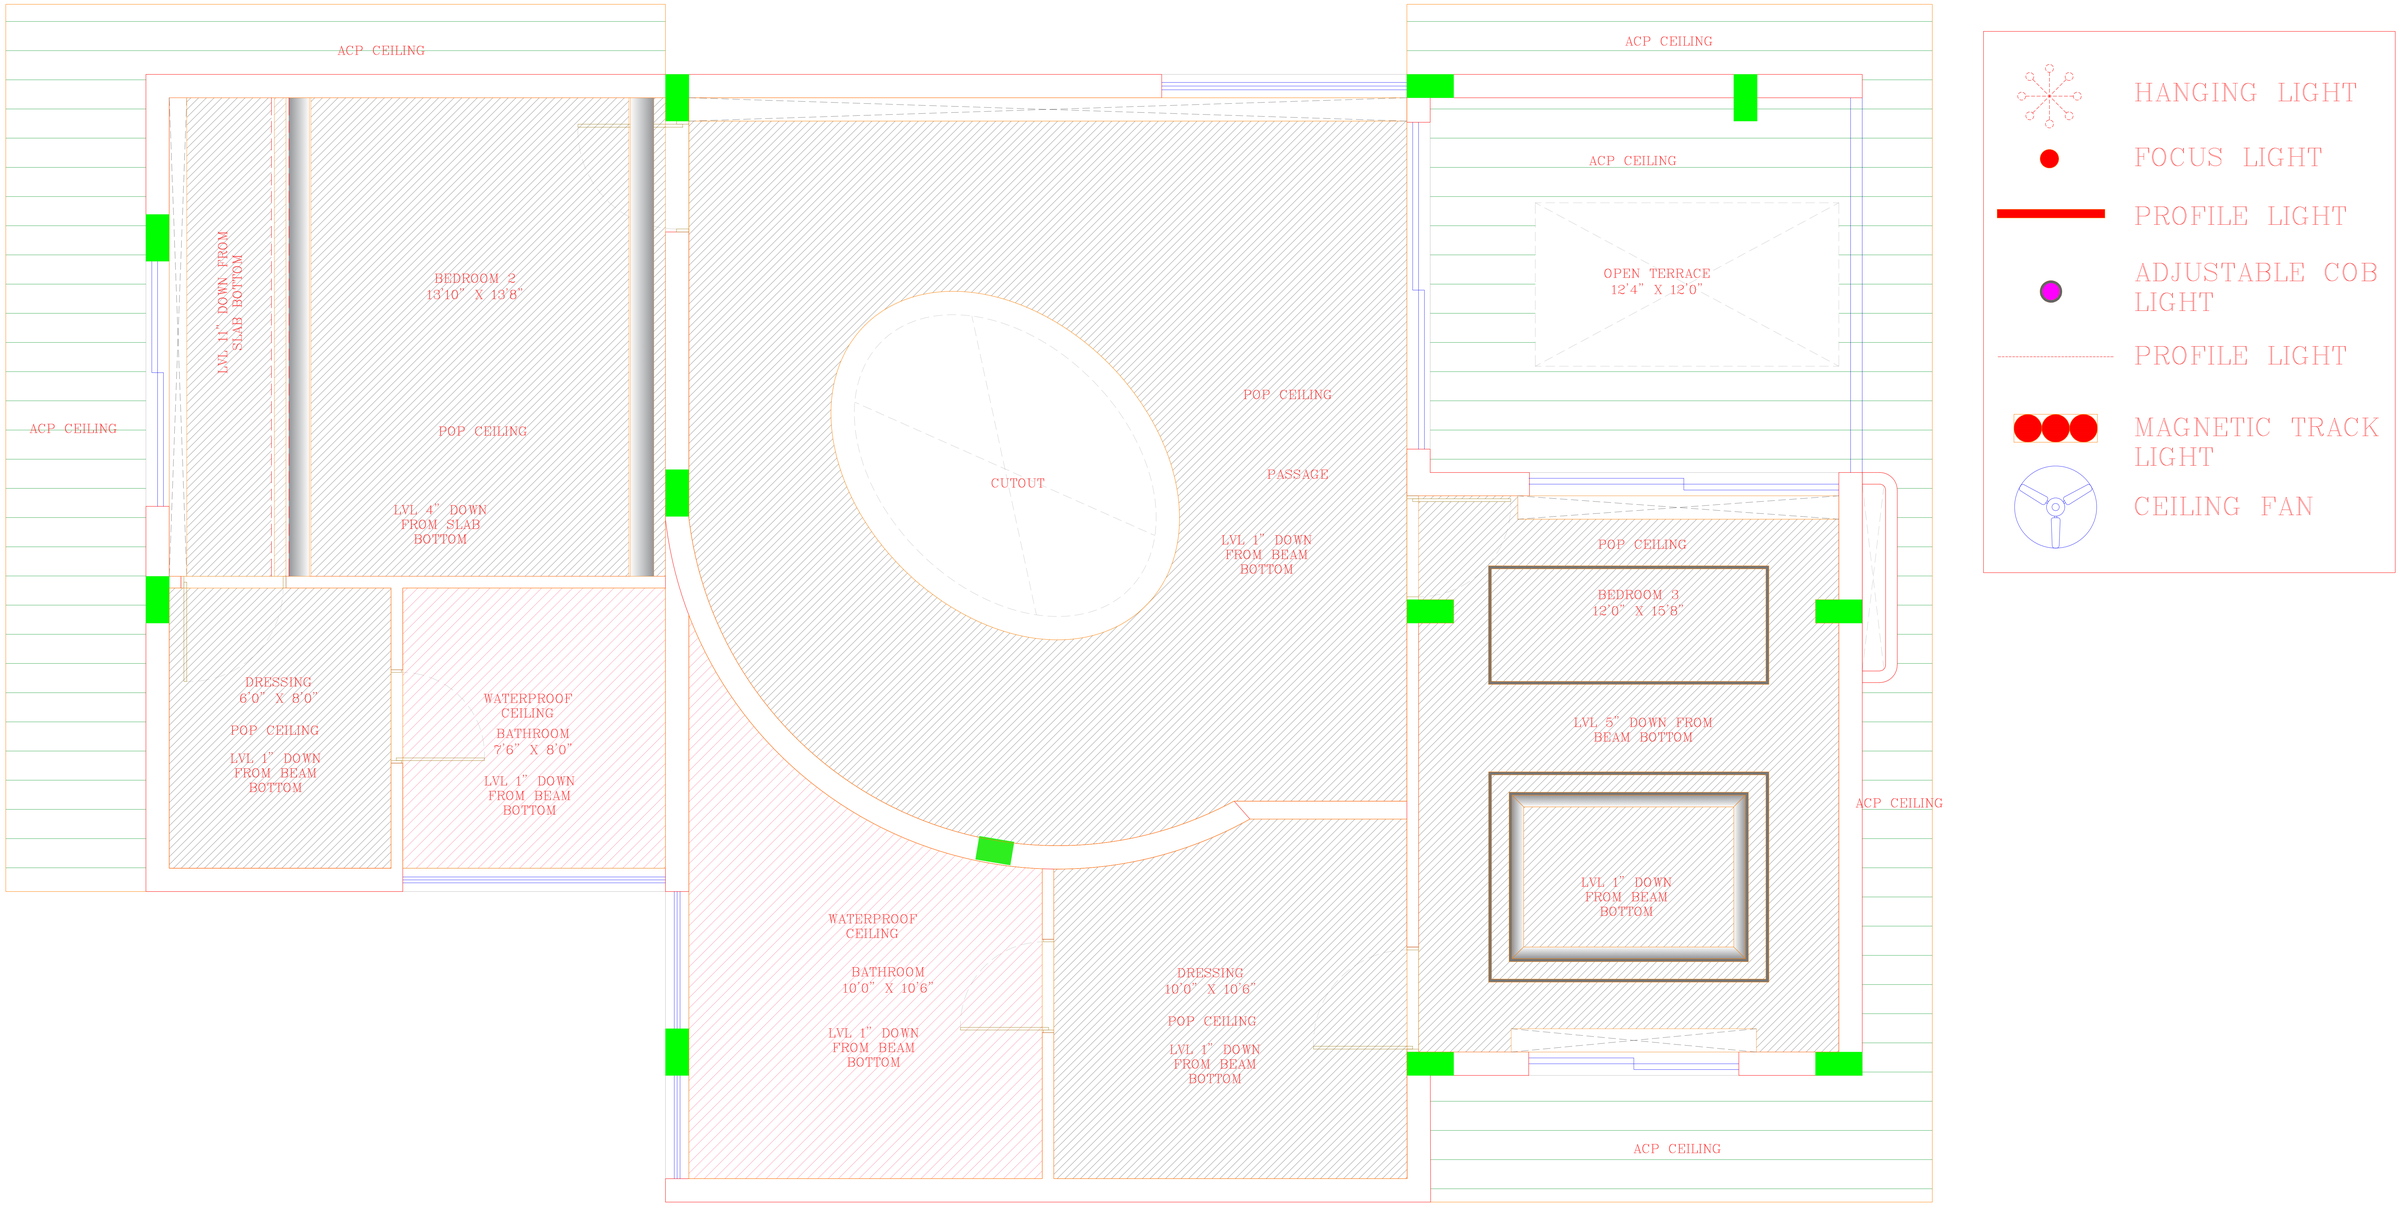


# FIRST FLOOR FALSE CEILING LAYOUT

PROPOSED LAYOUT FOR
MR.SANJAY JI

DESIGNED BY: AR. EKTA MISHRA

A4 A R C H I T E C T

NORTH

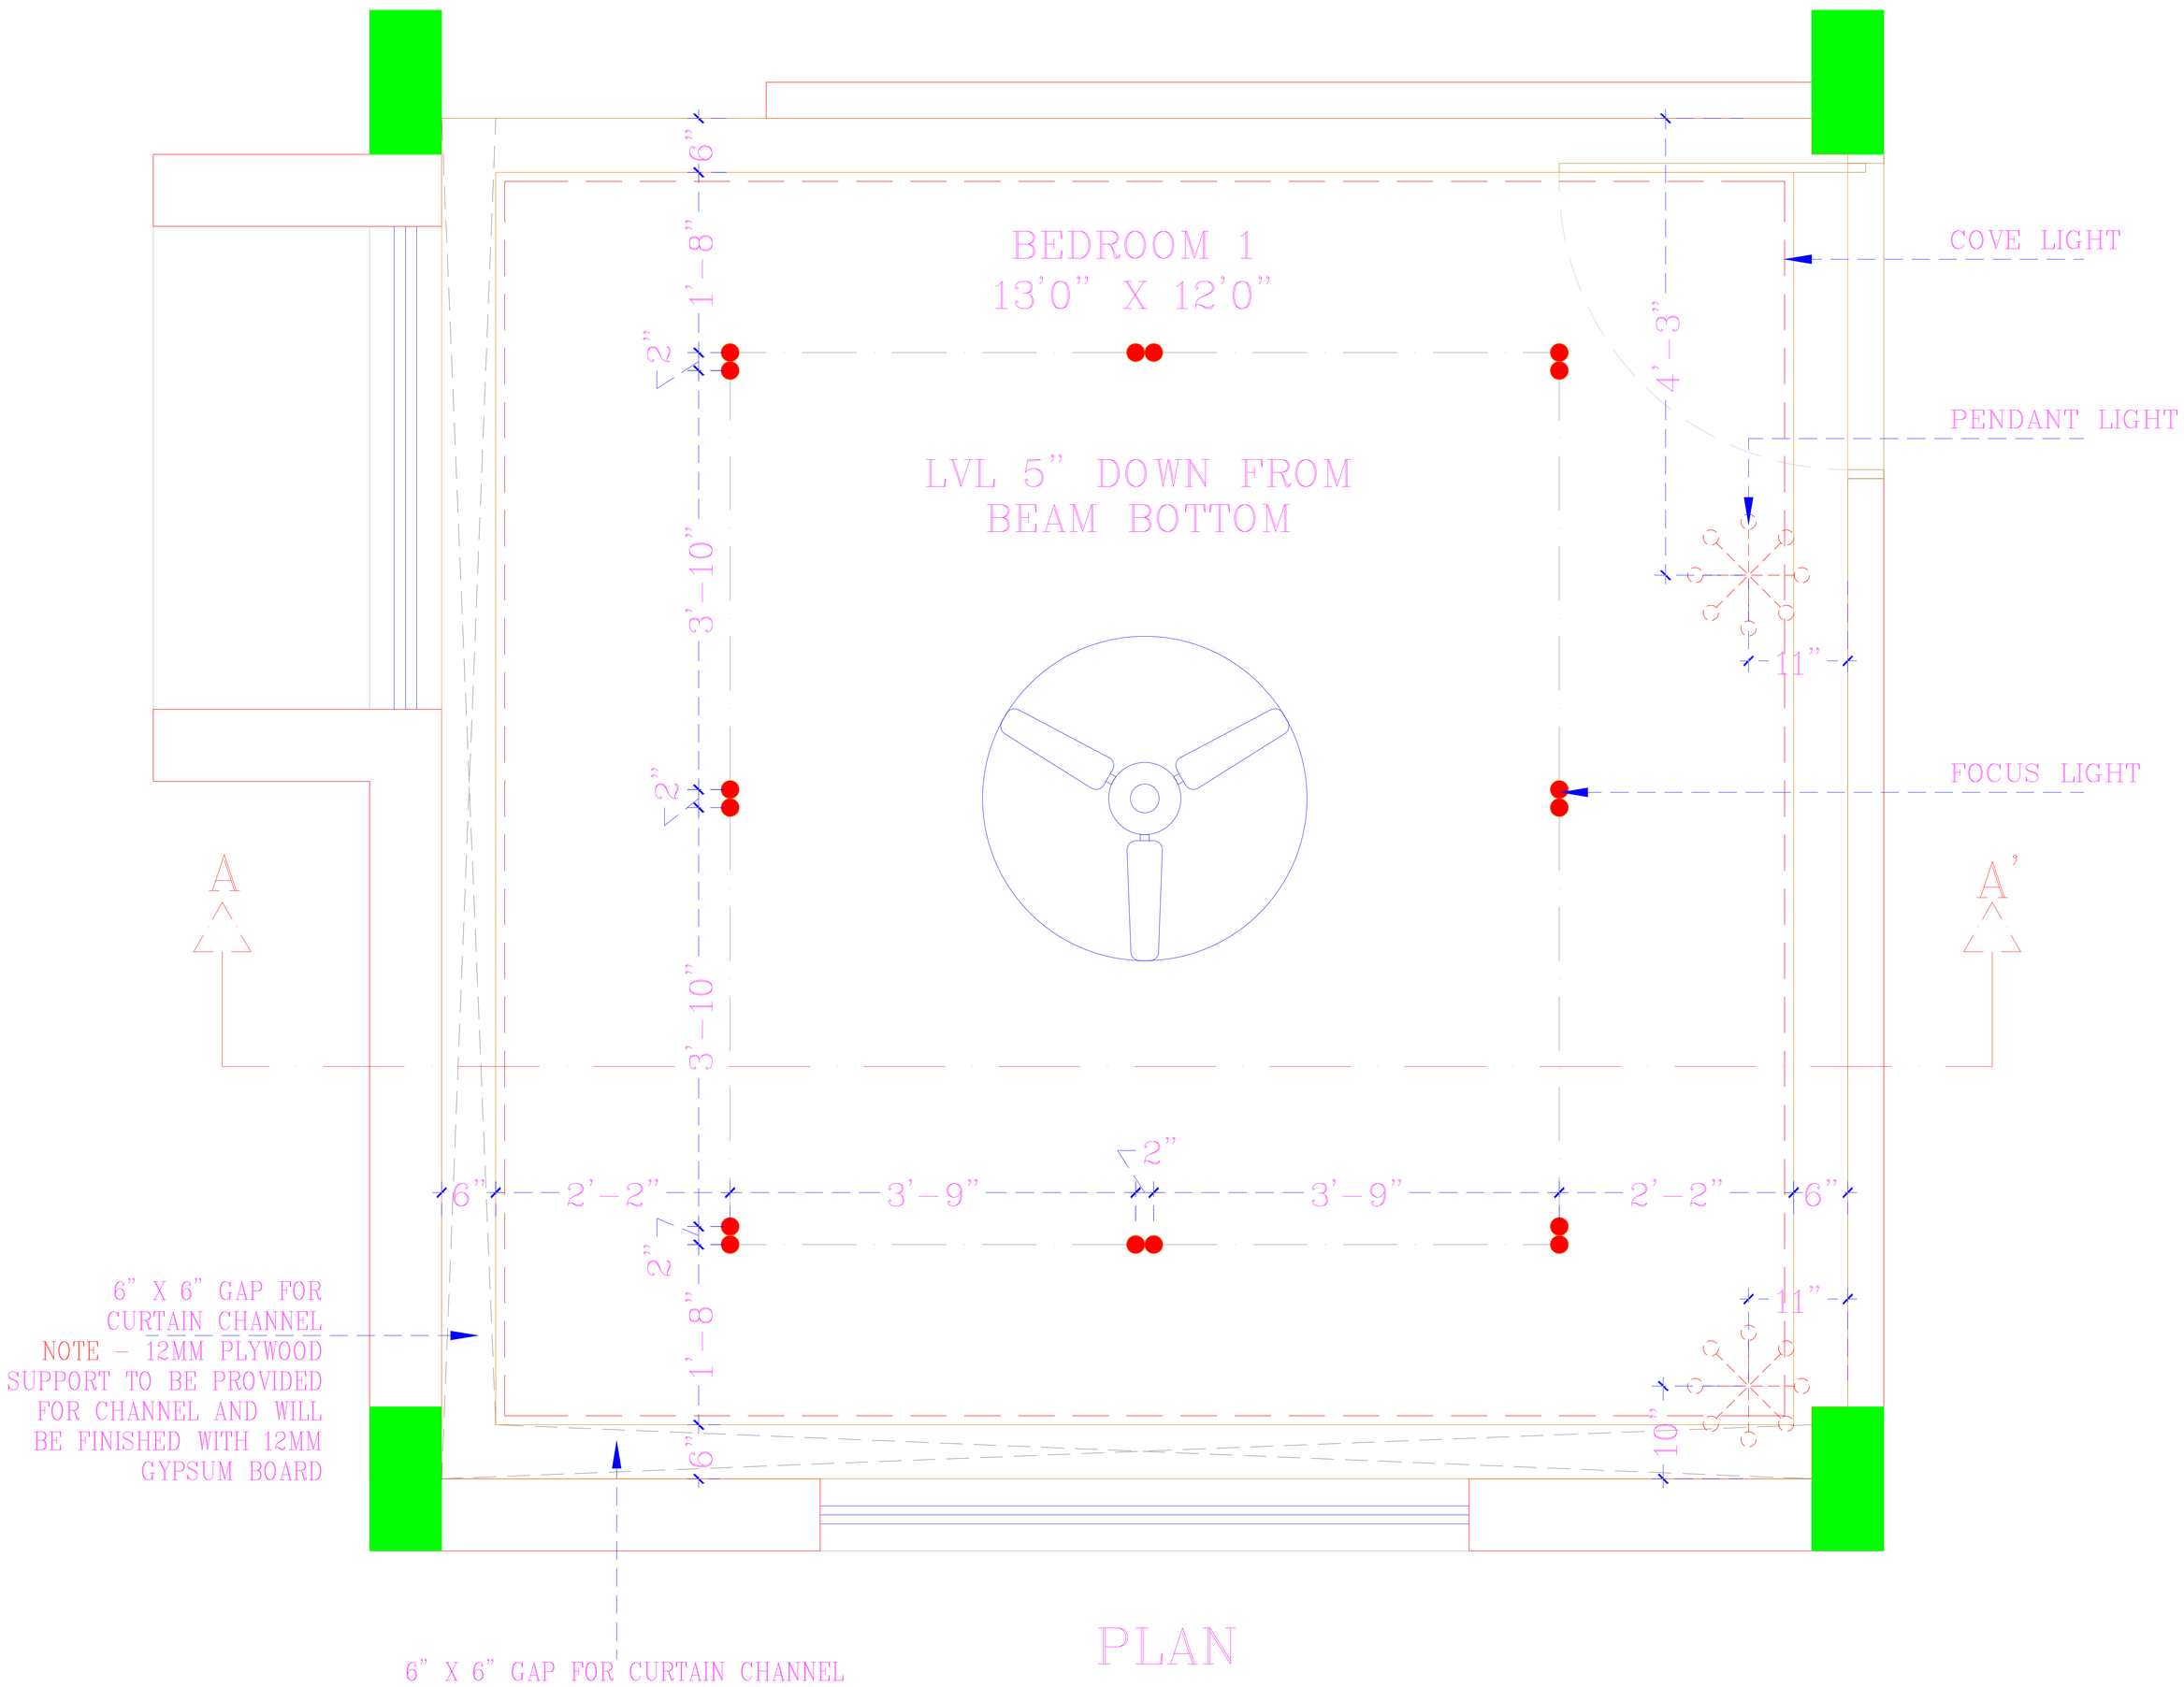


PLAN

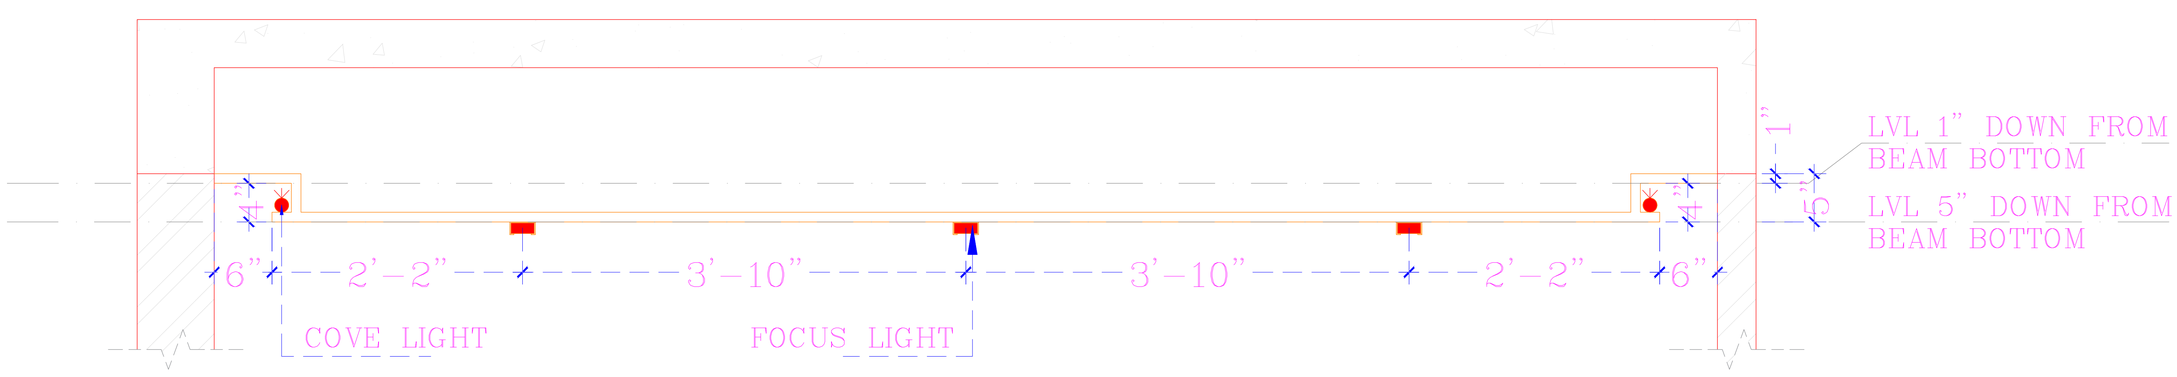


SECTION A-A'

REF. IMAGE

BEDROOM 1 FALSE
CEILING DESIGN

PROPOSED DESIGN FOR
MR. SANJAY JI

DESIGNED BY: AR. EKTA MISHRA

A 4 A R C H I T E C T

NORTH

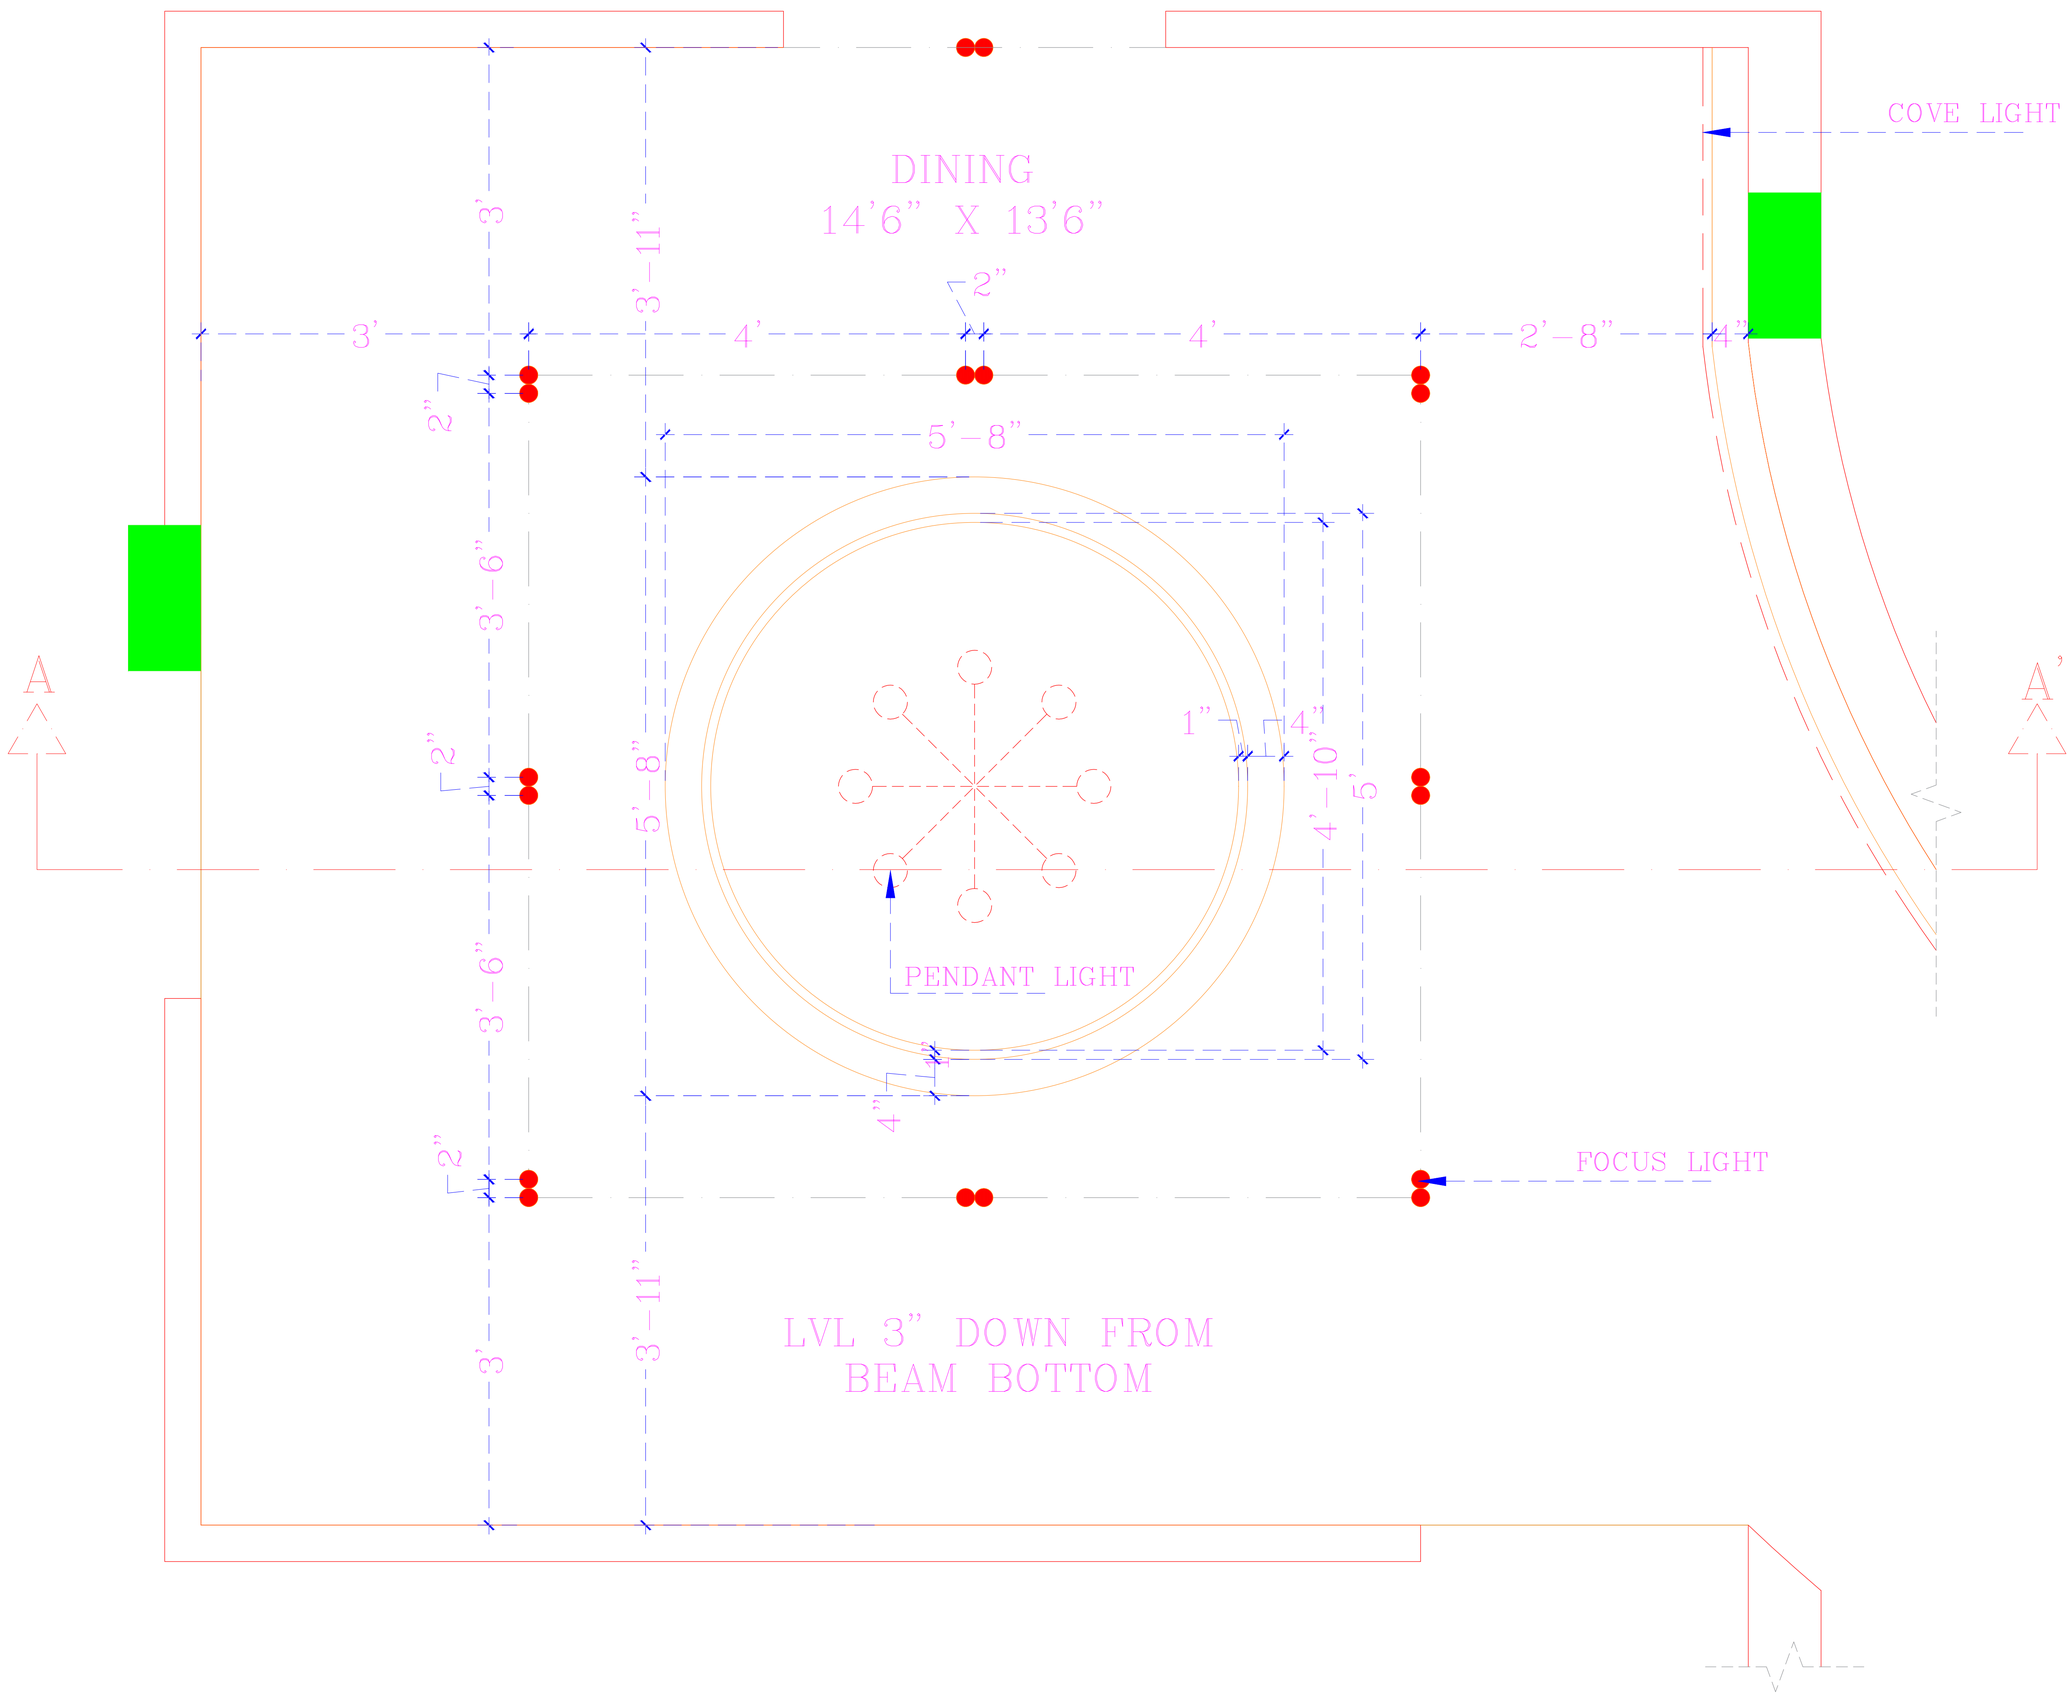


PLAN

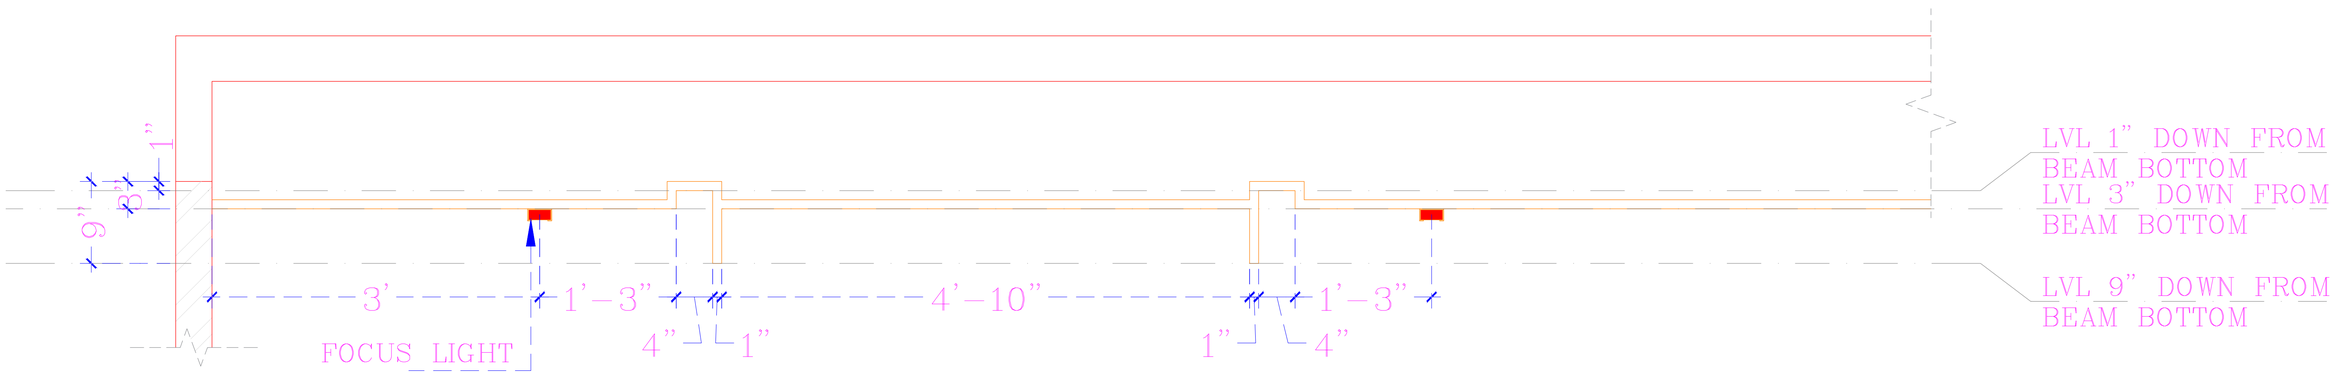


SECTION A-A'

REF. IMAGE

# DINING AREA FALSE CEILING DESIGN

PROPOSED DESIGN FOR
MR. SANJAY JI

DESIGNED BY: AR. EKTA MISHRA

A 4 A R C H I T E C T

NORTH

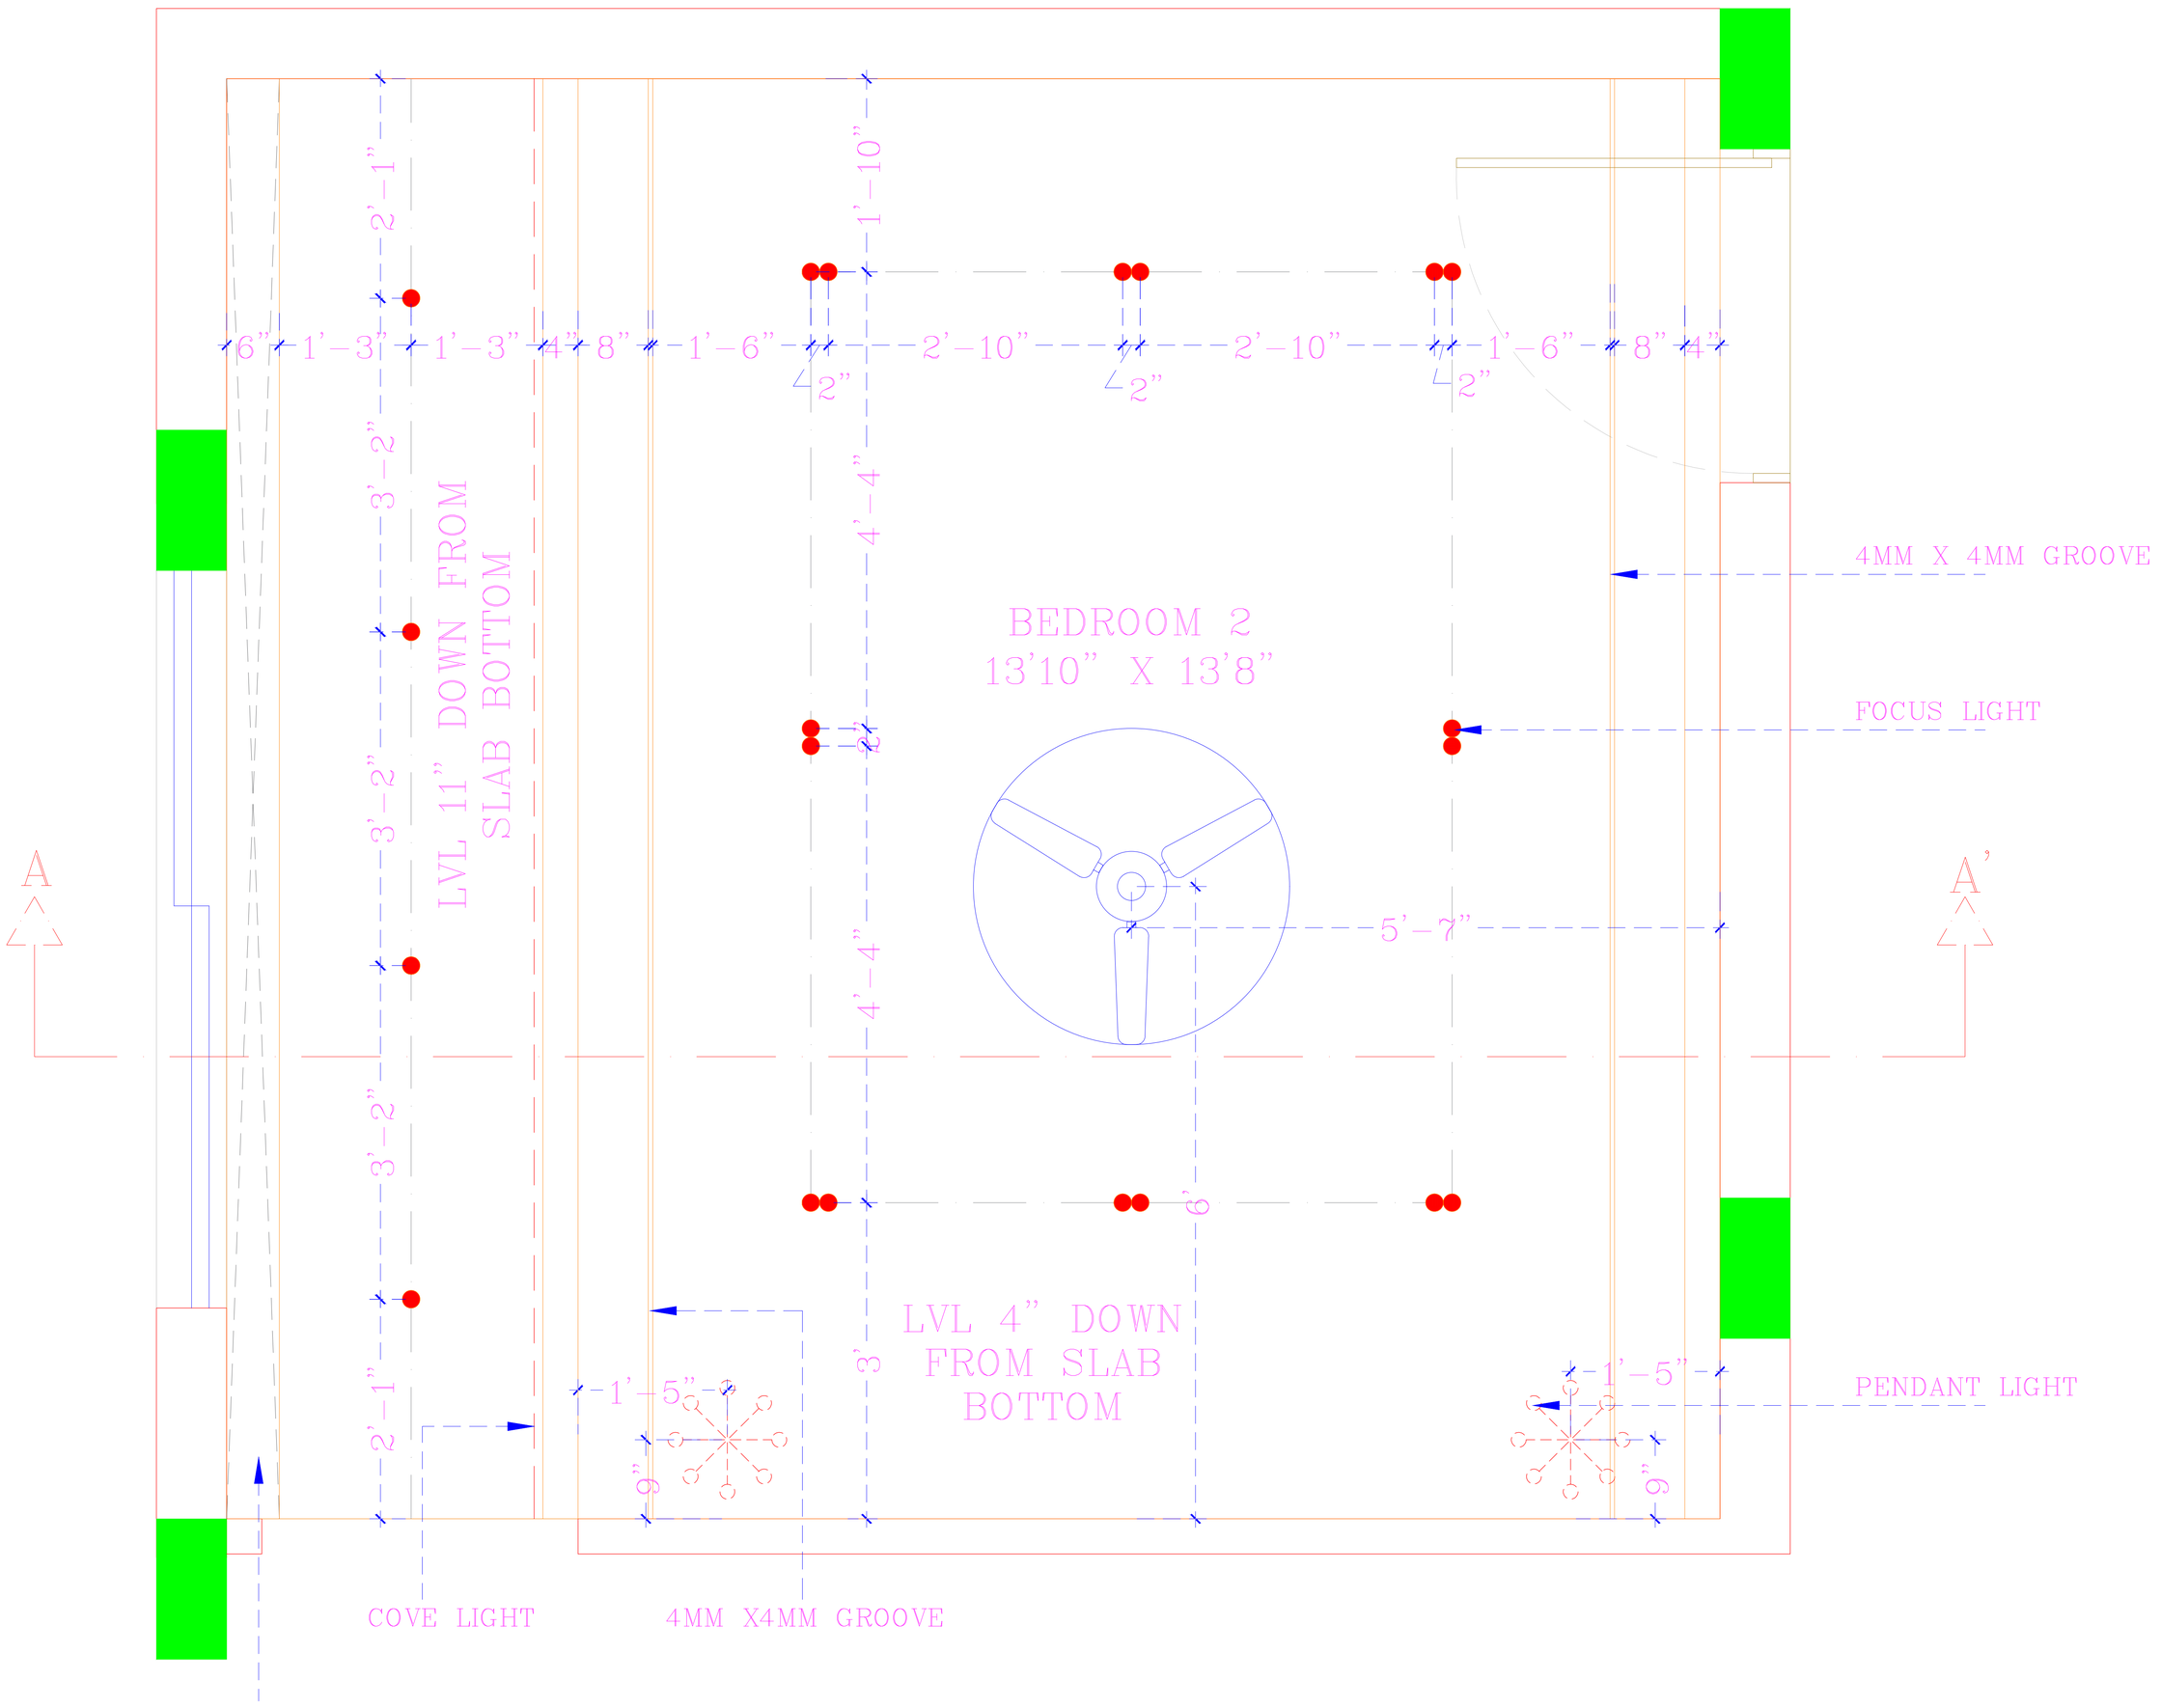


PLAN

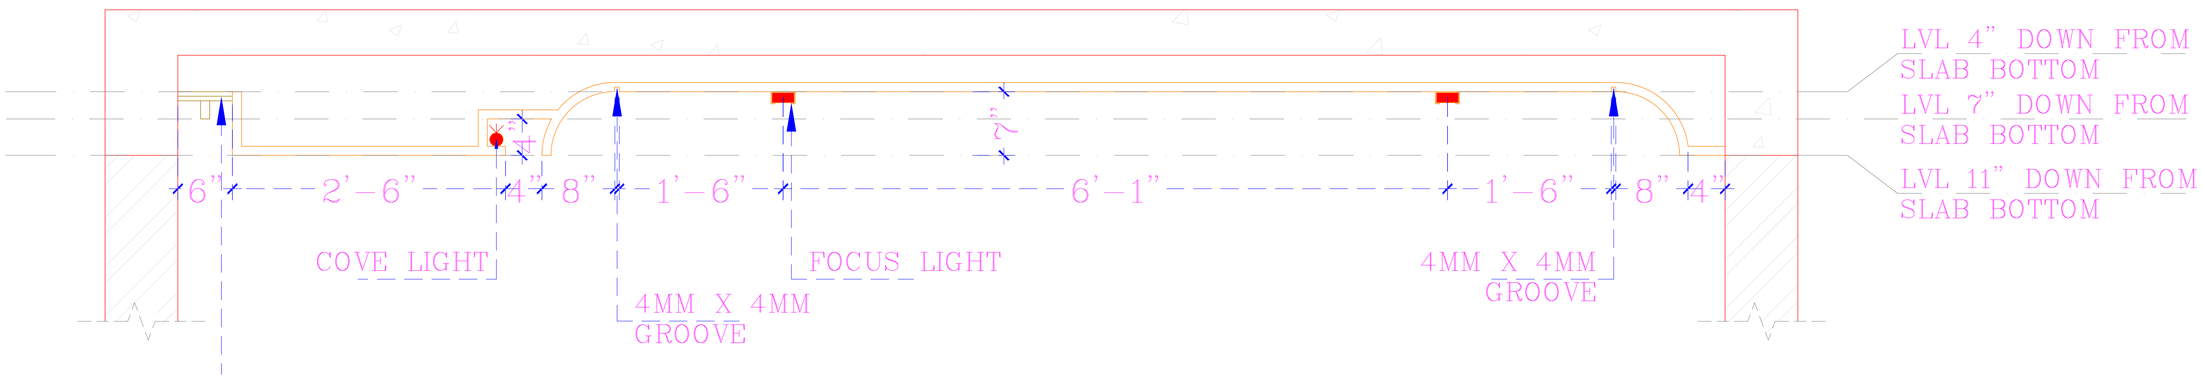


SECTION A-A'

REF. IMAGE

# BEDROOM 2 FALSE CEILING DESIGN

PROPOSED DESIGN FOR MR. SANJAY JI

DESIGNED BY: AR. EKTA MISHRA

A 4 A R C H I T E C T

NORTH

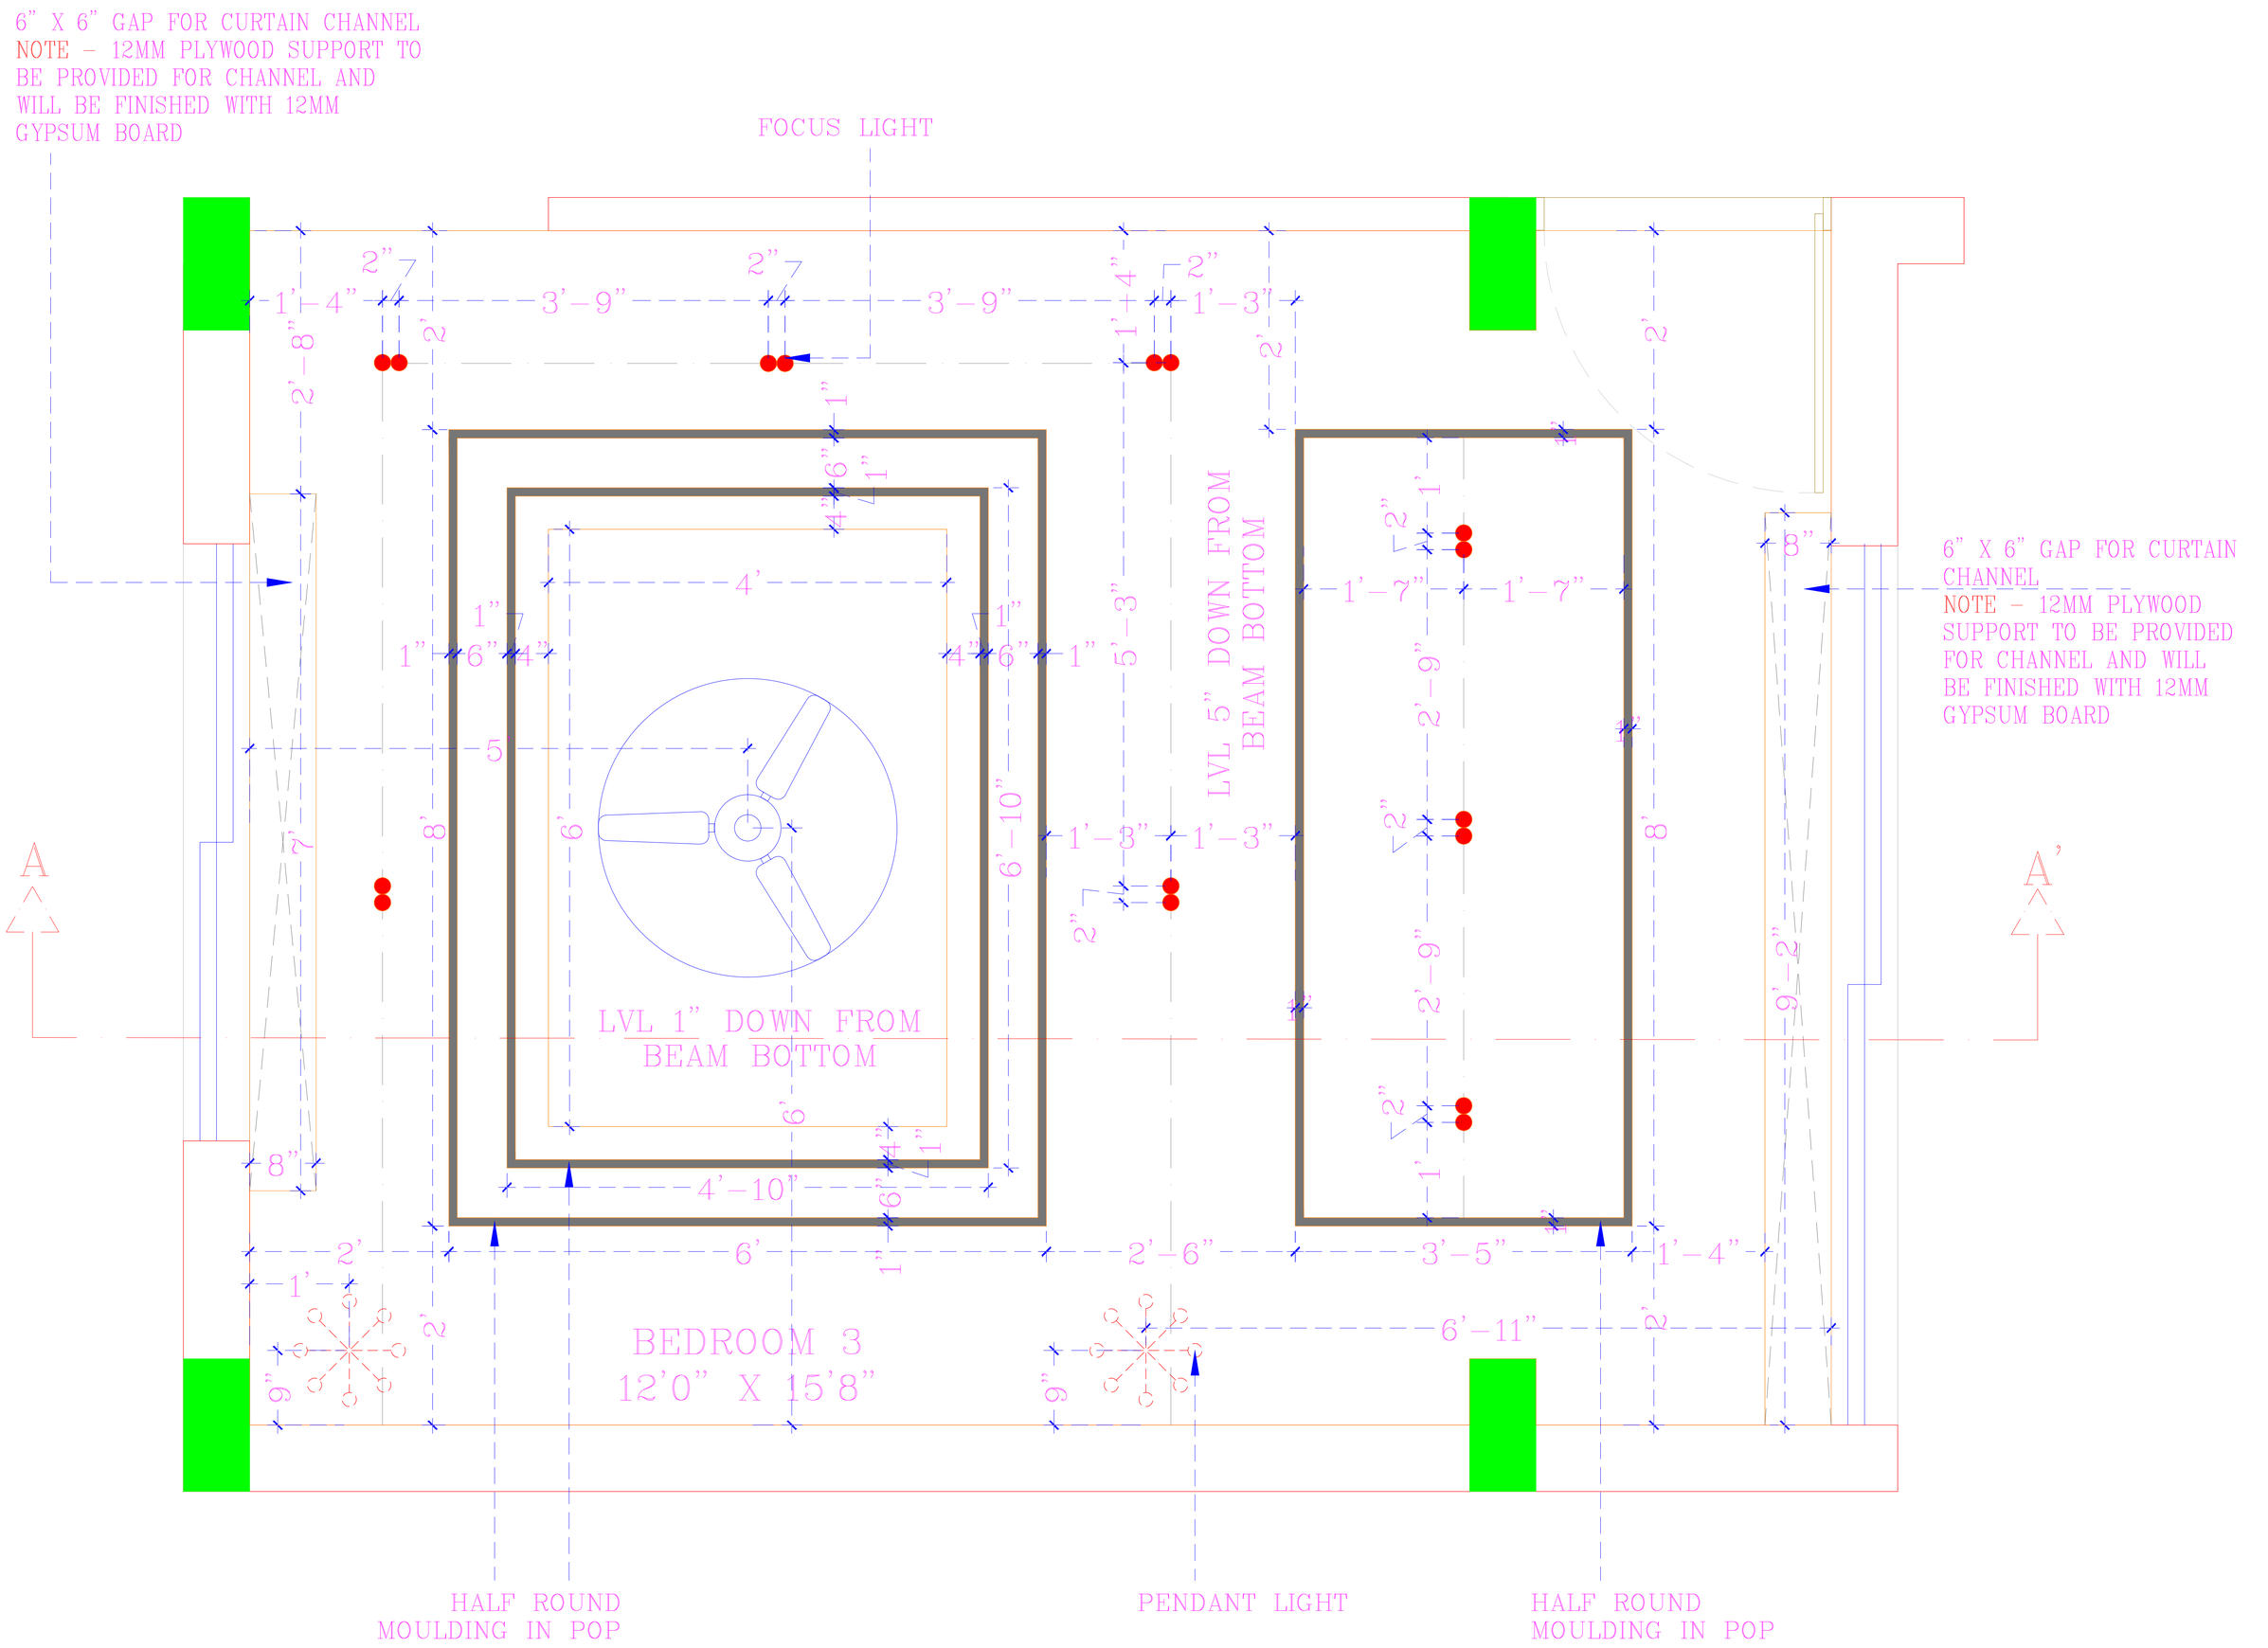


PLAN

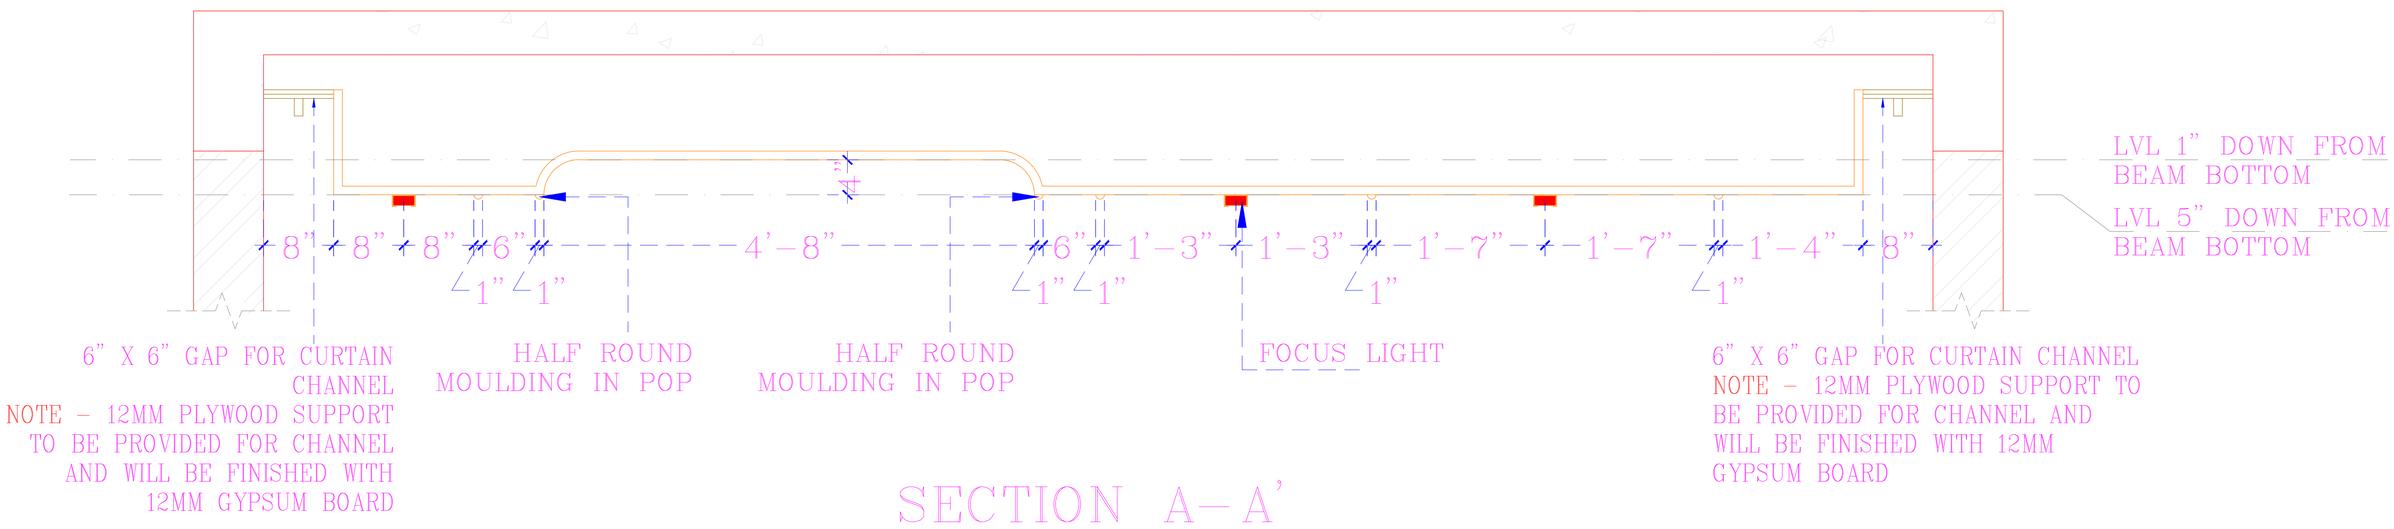


SECTION A-A'

REF. IMAGE FOR CURVE

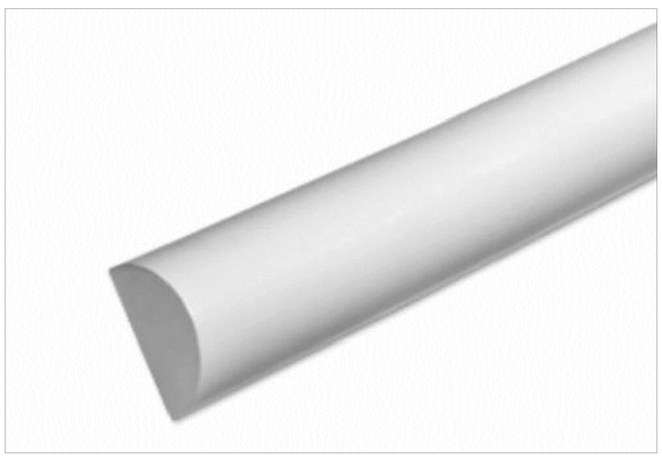

REF. IMAGE FOR HALF ROUND MOULDING

# BEDROOM 2 FALSE CEILING DESIGN

# PROPOSED DESIGN FOR MR. SANJAY JI

DESIGNED BY: AR. EKTA MISHRA

A 4 A R C H I T E C T

NORTH