STAIRCASE BEAM REINFORCEMENT DETAIL							
TYPE	BEAM SIZE	STEEL					RING
		BOTTOM	TOP	CENTER	BOTTOM EXTRA	TOP EXTRA	
B1	8" X 16"	2-16MM ø	2-16MM ø	2-16MM ø	2-12MM ø	3-12MM ø	8MM ø @150MM C/C
B2	8" X 16"	2-16MM ø	2-16MM ø	2-16MM ø	2-12MM ø	2-12MM ø	8MM ø @150MM C/C
B3	8" X 12"	2-16MM ø	2-16MM ø	2-16MM ø	2-12MM ø	2-12MM ø	8MM ø @150MM C/C
B4	6" X 16"	2-16MM ø	2-16MM ø	2-16MM ø	1-12MM ø	2-12MM ø	8MM ø @150MM C/C
B5	8" X 16"	2-16MM ø	2-16MM ø	2-16MM ø	3-12MM ø	2-12MM ø	8MM ø @150MM C/C

FIRST FLOOR SLAB REINFORCEMENT DETAIL						
TYPE	THICKNESS	STEEL				REMARKS
				EXTRA SUPPORT ON TOP		
		ALONG SHORT SPAN	ALONG LONG SPAN	ALONG SHORT SPAN	ALONG LONG SPAN	
S1	5"	10MMø@6"C/C	10MMø@6"C/C	10MMø@6"C/C	10MMø@12"C/C	TWO WAY
S2	5"	10MMø@6"C/C	10MMø@6"C/C	10MMø@6"C/C	10MMø@12"C/C	TWO WAY

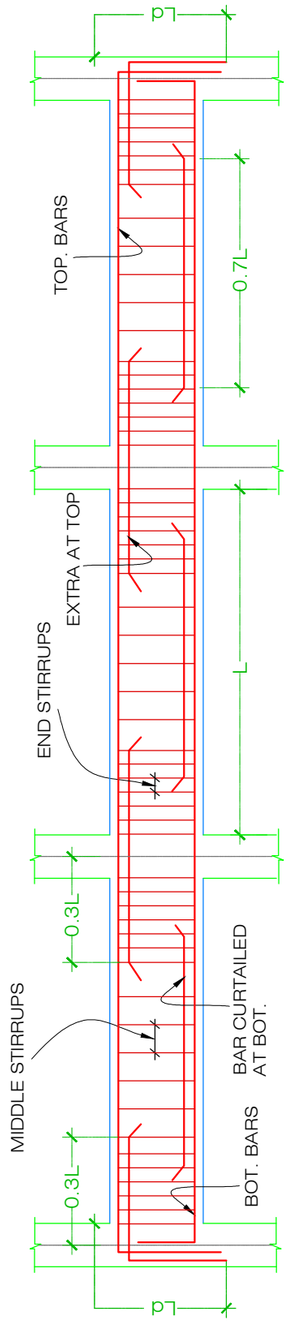

TYPICAL BEAM DETAIL

GROUND FLOOR BEAM AND SLAB REINFORCEMENT DETAIL

PROPOSED LAYOUT FOR MR.SANJAY JI

DESIGNED BY: AR. EKTA MISHRA

A4 A R C H I T E C T

NORTH

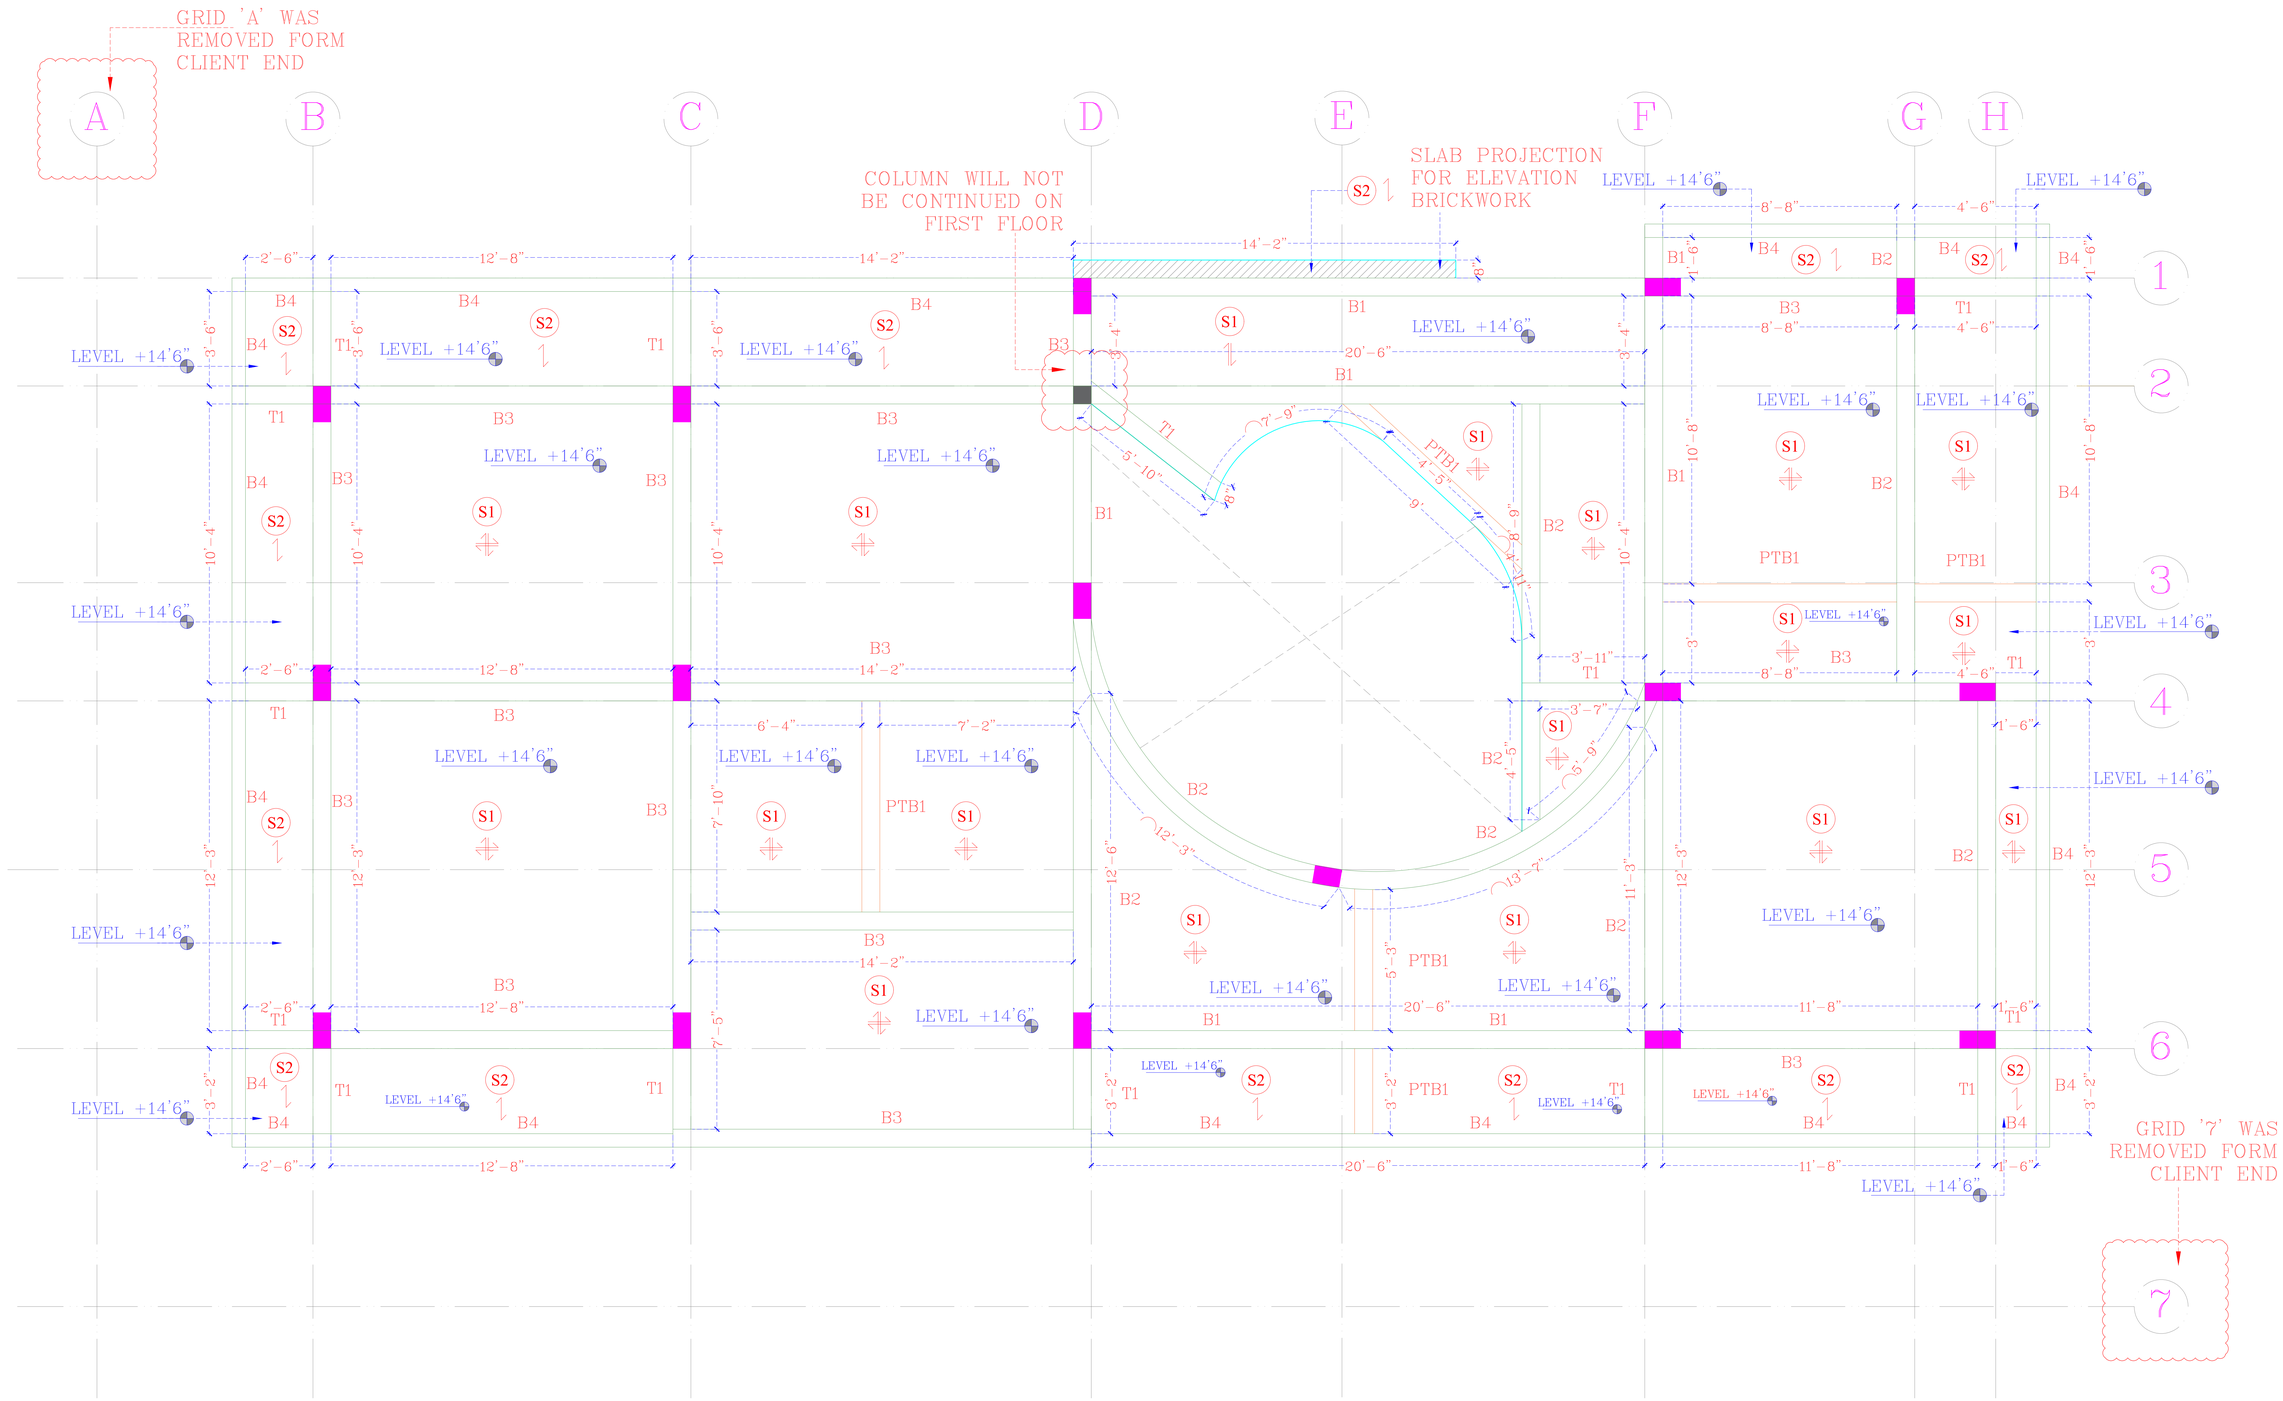

GROUND FLOOR SLAB DETAIL

PROPOSED LAYOUT FOR
MR.SANJAY JI

DESIGNED BY: AR. EKTA MISHRA

A4 A R C H I T E C T

NORTH