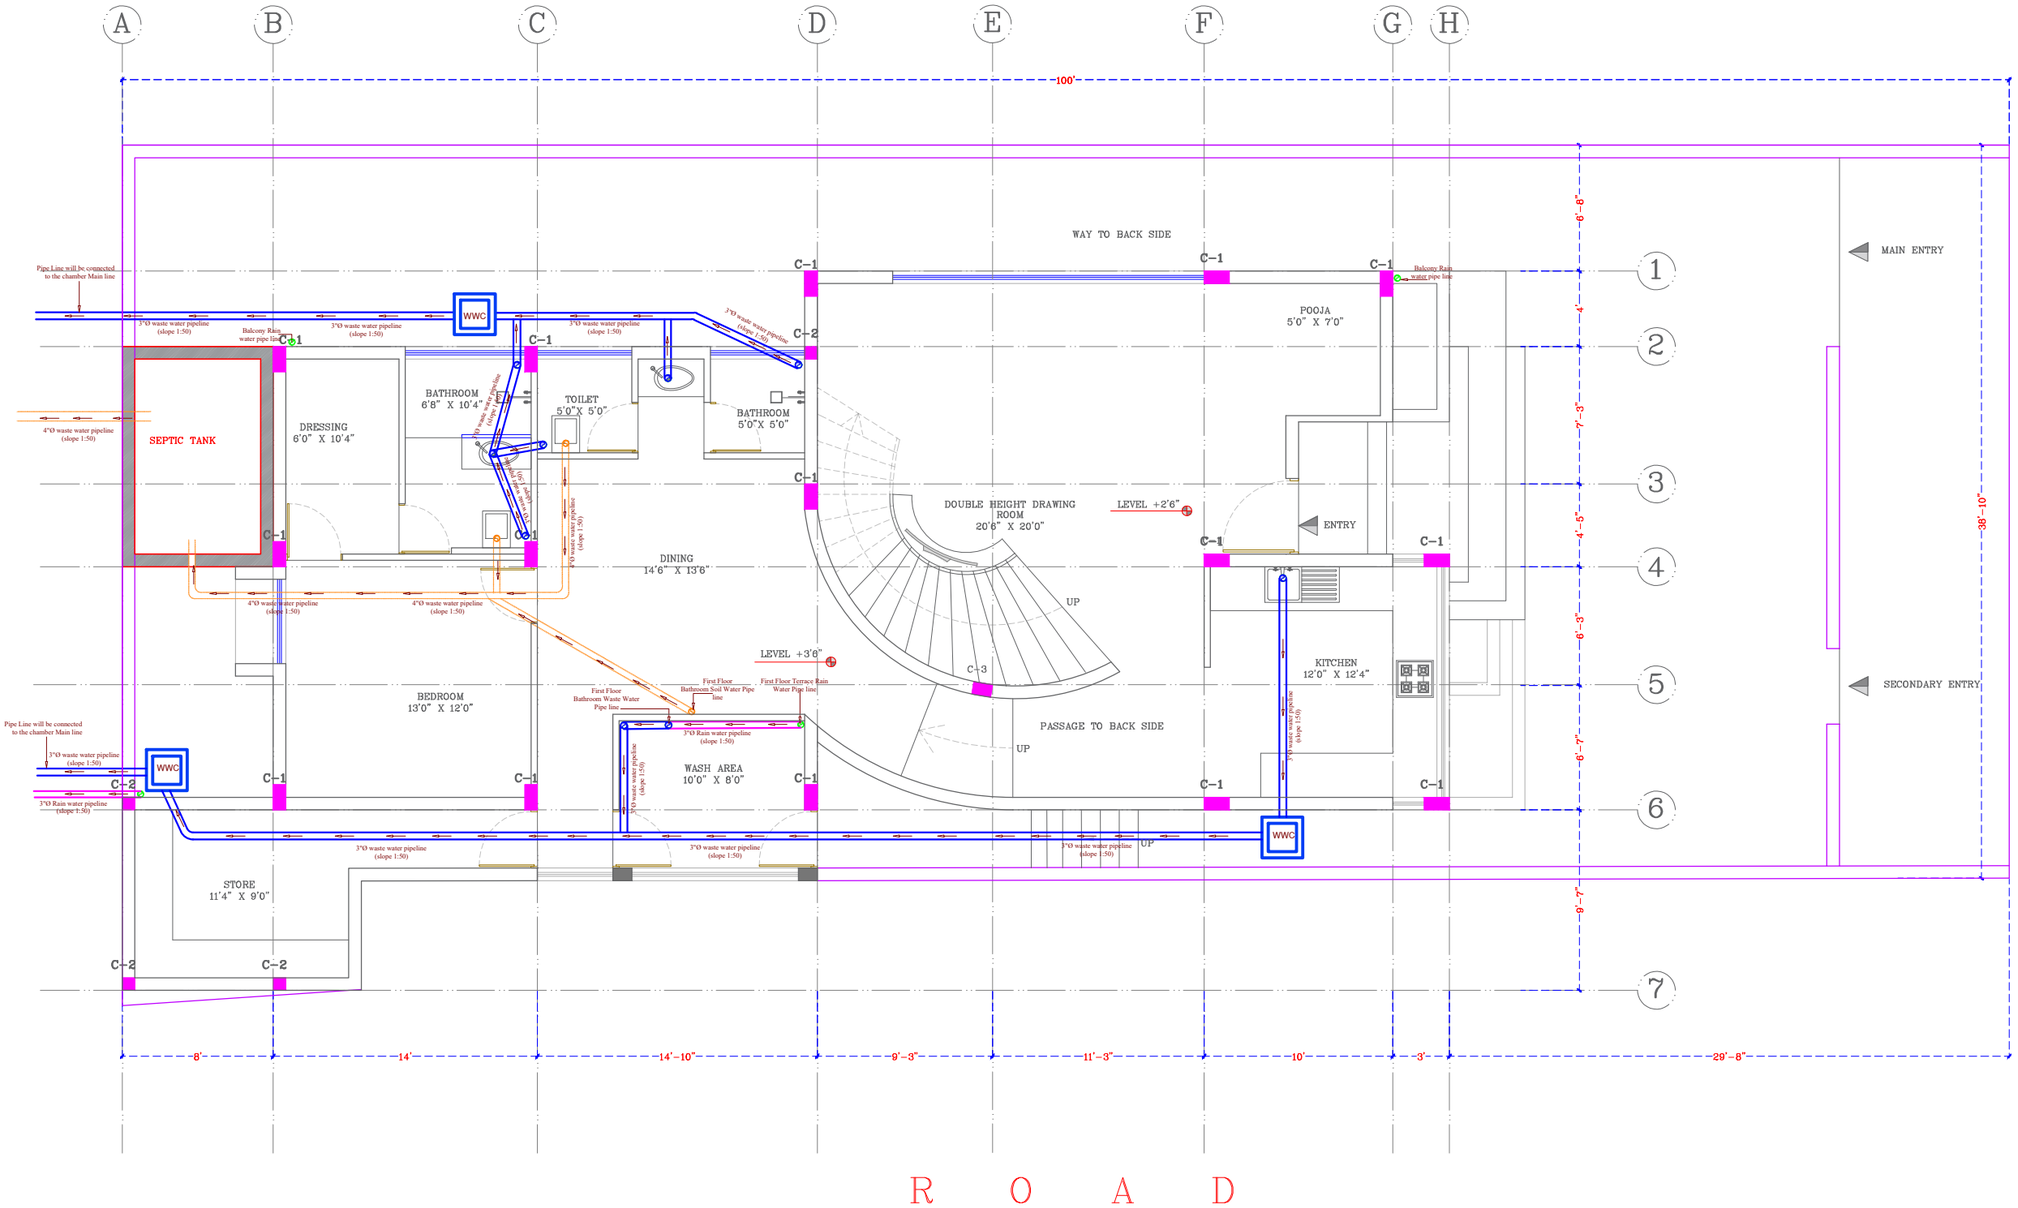

LEGEND - PLUMBING

	PLUMBING SOIL WATER
	PLUMBING RAIN WATER
	PLUMBING WASTE WATER
	4" SOIL WATER LINE
	3" WASTE WATER LINE
	3" RAIN WATER LINE
SWC	450 X 450 MM SOIL WATER CHAMBER (SWC)
WWC	450 X 450 MM WASTE WATER CHAMBER (WWC)
RWC	450 X 450 MM RAIN WATER CHAMBER (RWC)

GROUND FLOOR PLUMBING LAYOUT PLAN

PROPOSED LAYOUT FOR
MR.SANJAY JI

DESIGNED BY: AR. EKTA MISHRA

A4 A R C H I T E C T

NORTH

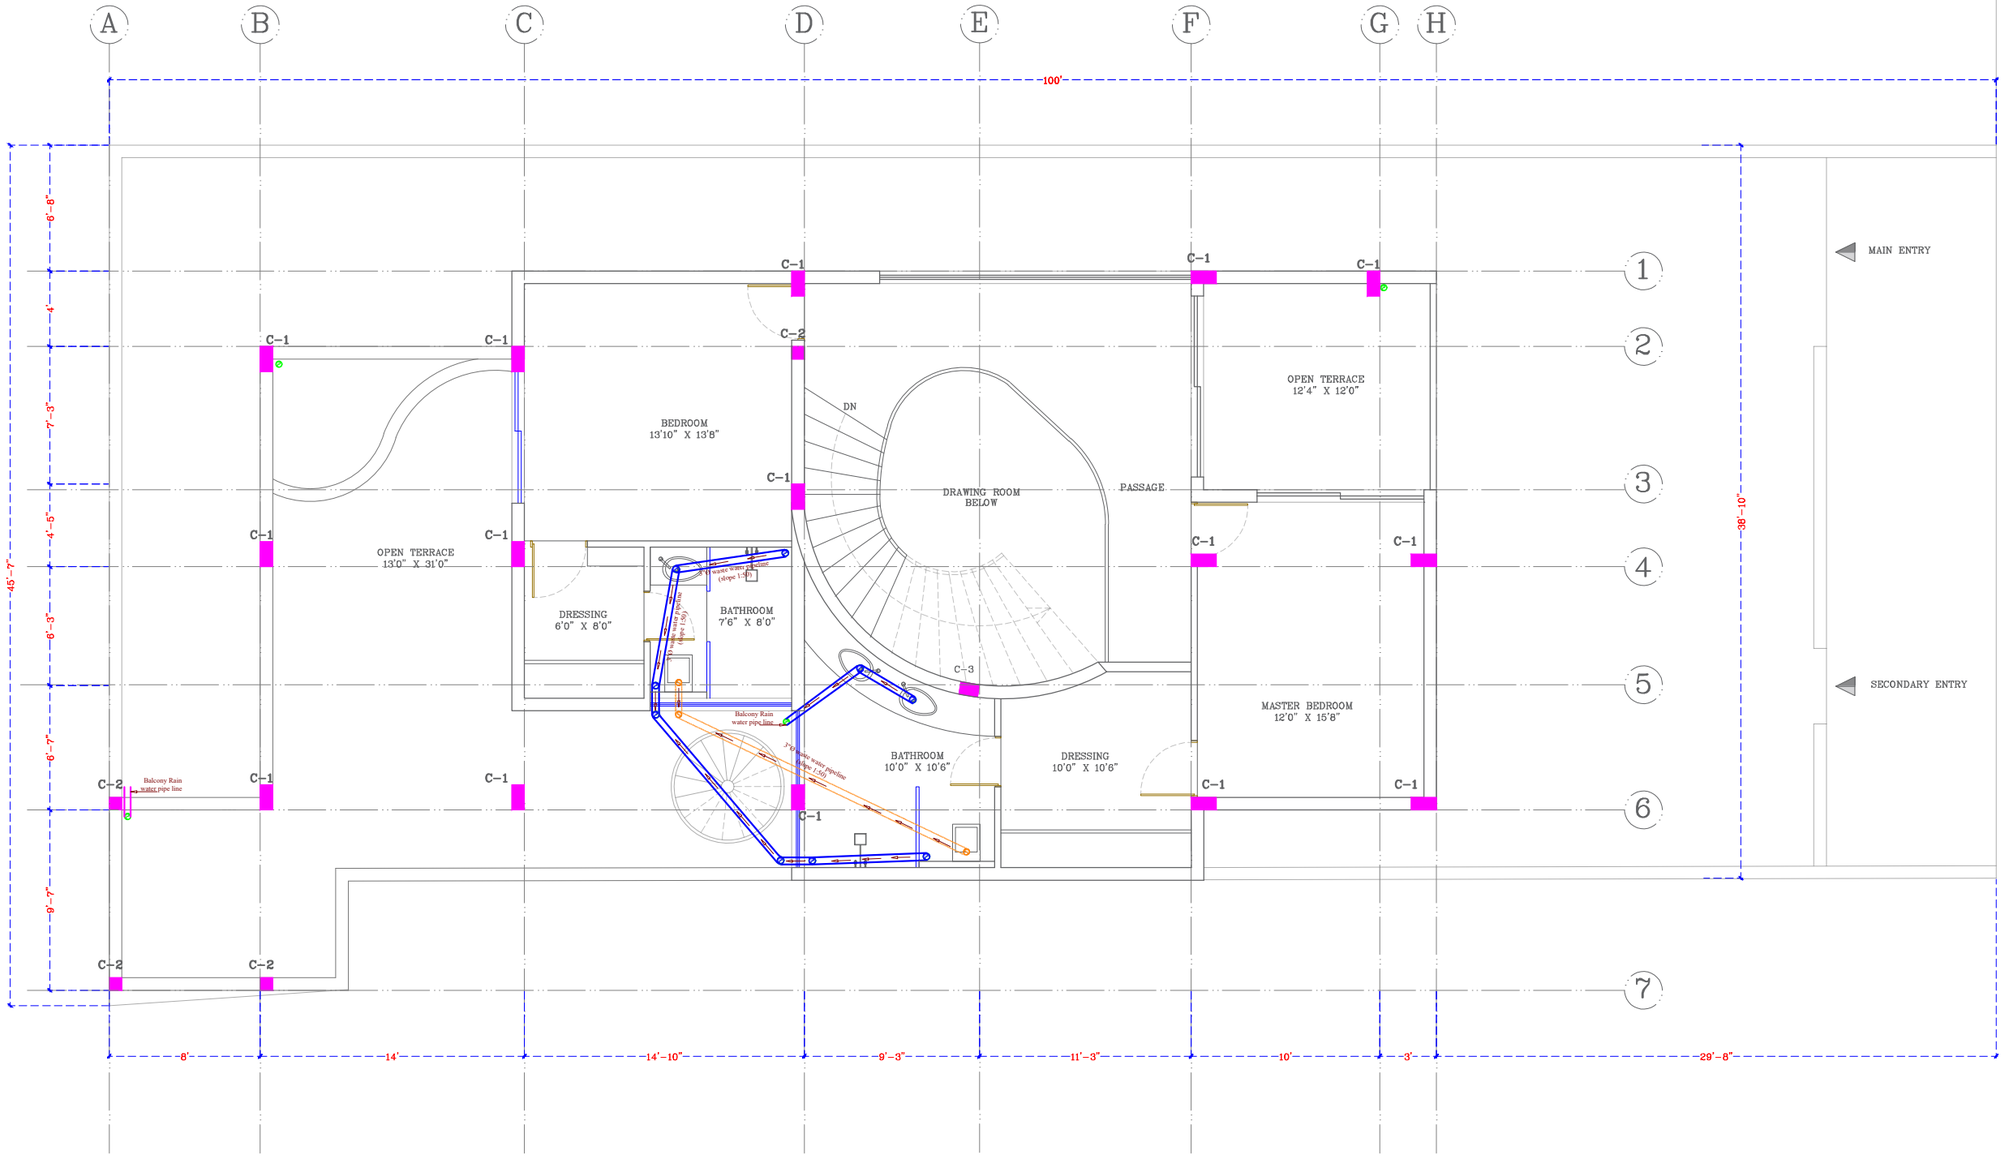

LEGEND - PLUMBING

	PLUMBING SOIL WATER
	PLUMBING RAIN WATER
	PLUMBING WASTE WATER
	4" SOIL WATER LINE
	3" WASTE WATER LINE
	3" RAIN WATER LINE
SWC	450 X 450 MM SOIL WATER CHAMBER (SWC)
WWC	450 X 450 MM WASTE WATER CHAMBER (WWC)
RWC	450 X 450 MM RAIN WATER CHAMBER (RWC)

FIRST FLOOR PLUMBING LAYOUT PLAN

PROPOSED LAYOUT FOR
MR.SANJAY JI

DESIGNED BY: AR. EKTA MISHRA

A4 A R C H I T E C T

NORTH