			LEVEL (UNLESS MENTION)				LEVEL (UNLESS MENTION)
		ELECTRICAL	BOTTOM OF SWITCH PLATE			ELECTRICAL	BOTTOM OF SWITCH PLATE
1	M	MASTER SWITCH (KEY SWITCH)	+4' HT. FROM FFL	14		INVERTER	AS/DETAIL
2		SWITCH BOARD WITH 5/15 AMP SOCKET (8 MODULE/6 MODULE)	+4' HT. FROM FFL	15		WI-FI ROUTER	
3		TWO WAY SWITCH	+4' HT. FROM FFL	16	V D P	VIDEO DOOR PHONE	+4' HT. FROM FFL
4	D.B	DISTRIBUTION BOARD	+8' HT. FROM FFL	17		BELL PUSH	+3'6" HT. FROM FFL
5	A C	AC OPERATING SWITCH	AS/AC LOCATION	18		BELL BUZZER	+8' HT. FROM FFL
6	32	32 AMP WITH SWITCH & SOCKET	+1' HT. FROM FFL	19		EXHAUST FAN	AS/DETAIL
7	16	16 AMP WITH SWITCH & SOCKET	+1' HT. FROM FFL	20		BED SIDE TABLE SET	+2' HT. FROM FFL
8	G	GEYSER	+8' HT. FROM FFL	21		BED SIDE TABLE SET	+2' HT. FROM FFL
9		WALL FAN	+5' HT. FROM FFL	22		TV SET	+4' HT. FROM FFL
10		BRACKET LIGHT	+8' HT. FROM FFL	23		TV SET	+2' HT. FROM FFL
11		FLOOR LIGHT	+1' HT. FROM FFL	24		CCTV	ON CEILING
12		WARDROBE INTERNAL LIGHT	+5' HT. FROM FFL	25	AC	A.C (INDOOR UNIT)	
13	BRW	BOREWELL		26	R.C	RAW CABLE	
				27	M	MOTOR POINT	

ELECTRICAL LEGENDS

PROPOSED RESIDENCE FOR
MR. SANJAY JI

DESIGNED BY: AR. EKTA MISHRA

A4 A R C H I T E C T

NORTH

NORTH

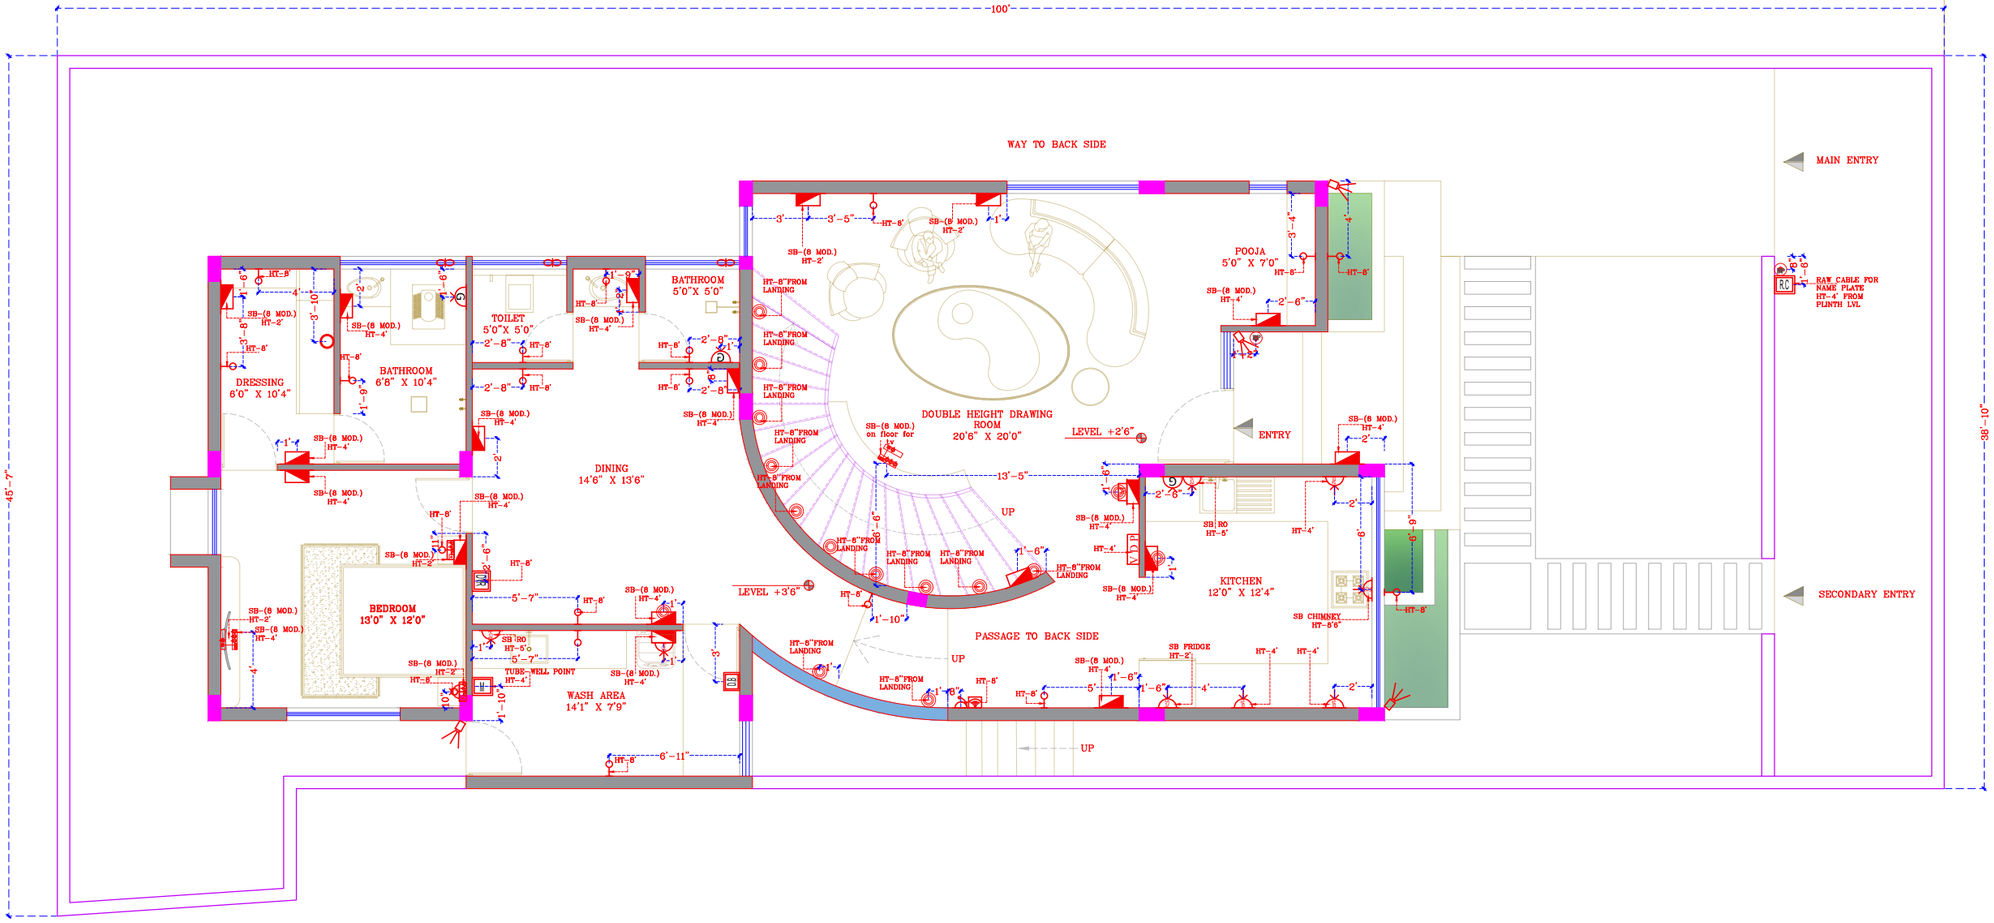

R O A D

WEST

R O A D

EAST

SOUTH

GROUND FLOOR PLAN

PROPOSED LAYOUT FOR
MR.SANJAY JI

DESIGNED BY: AR. EKTA MISHRA

A4 A R C H I T E C T

NORTH

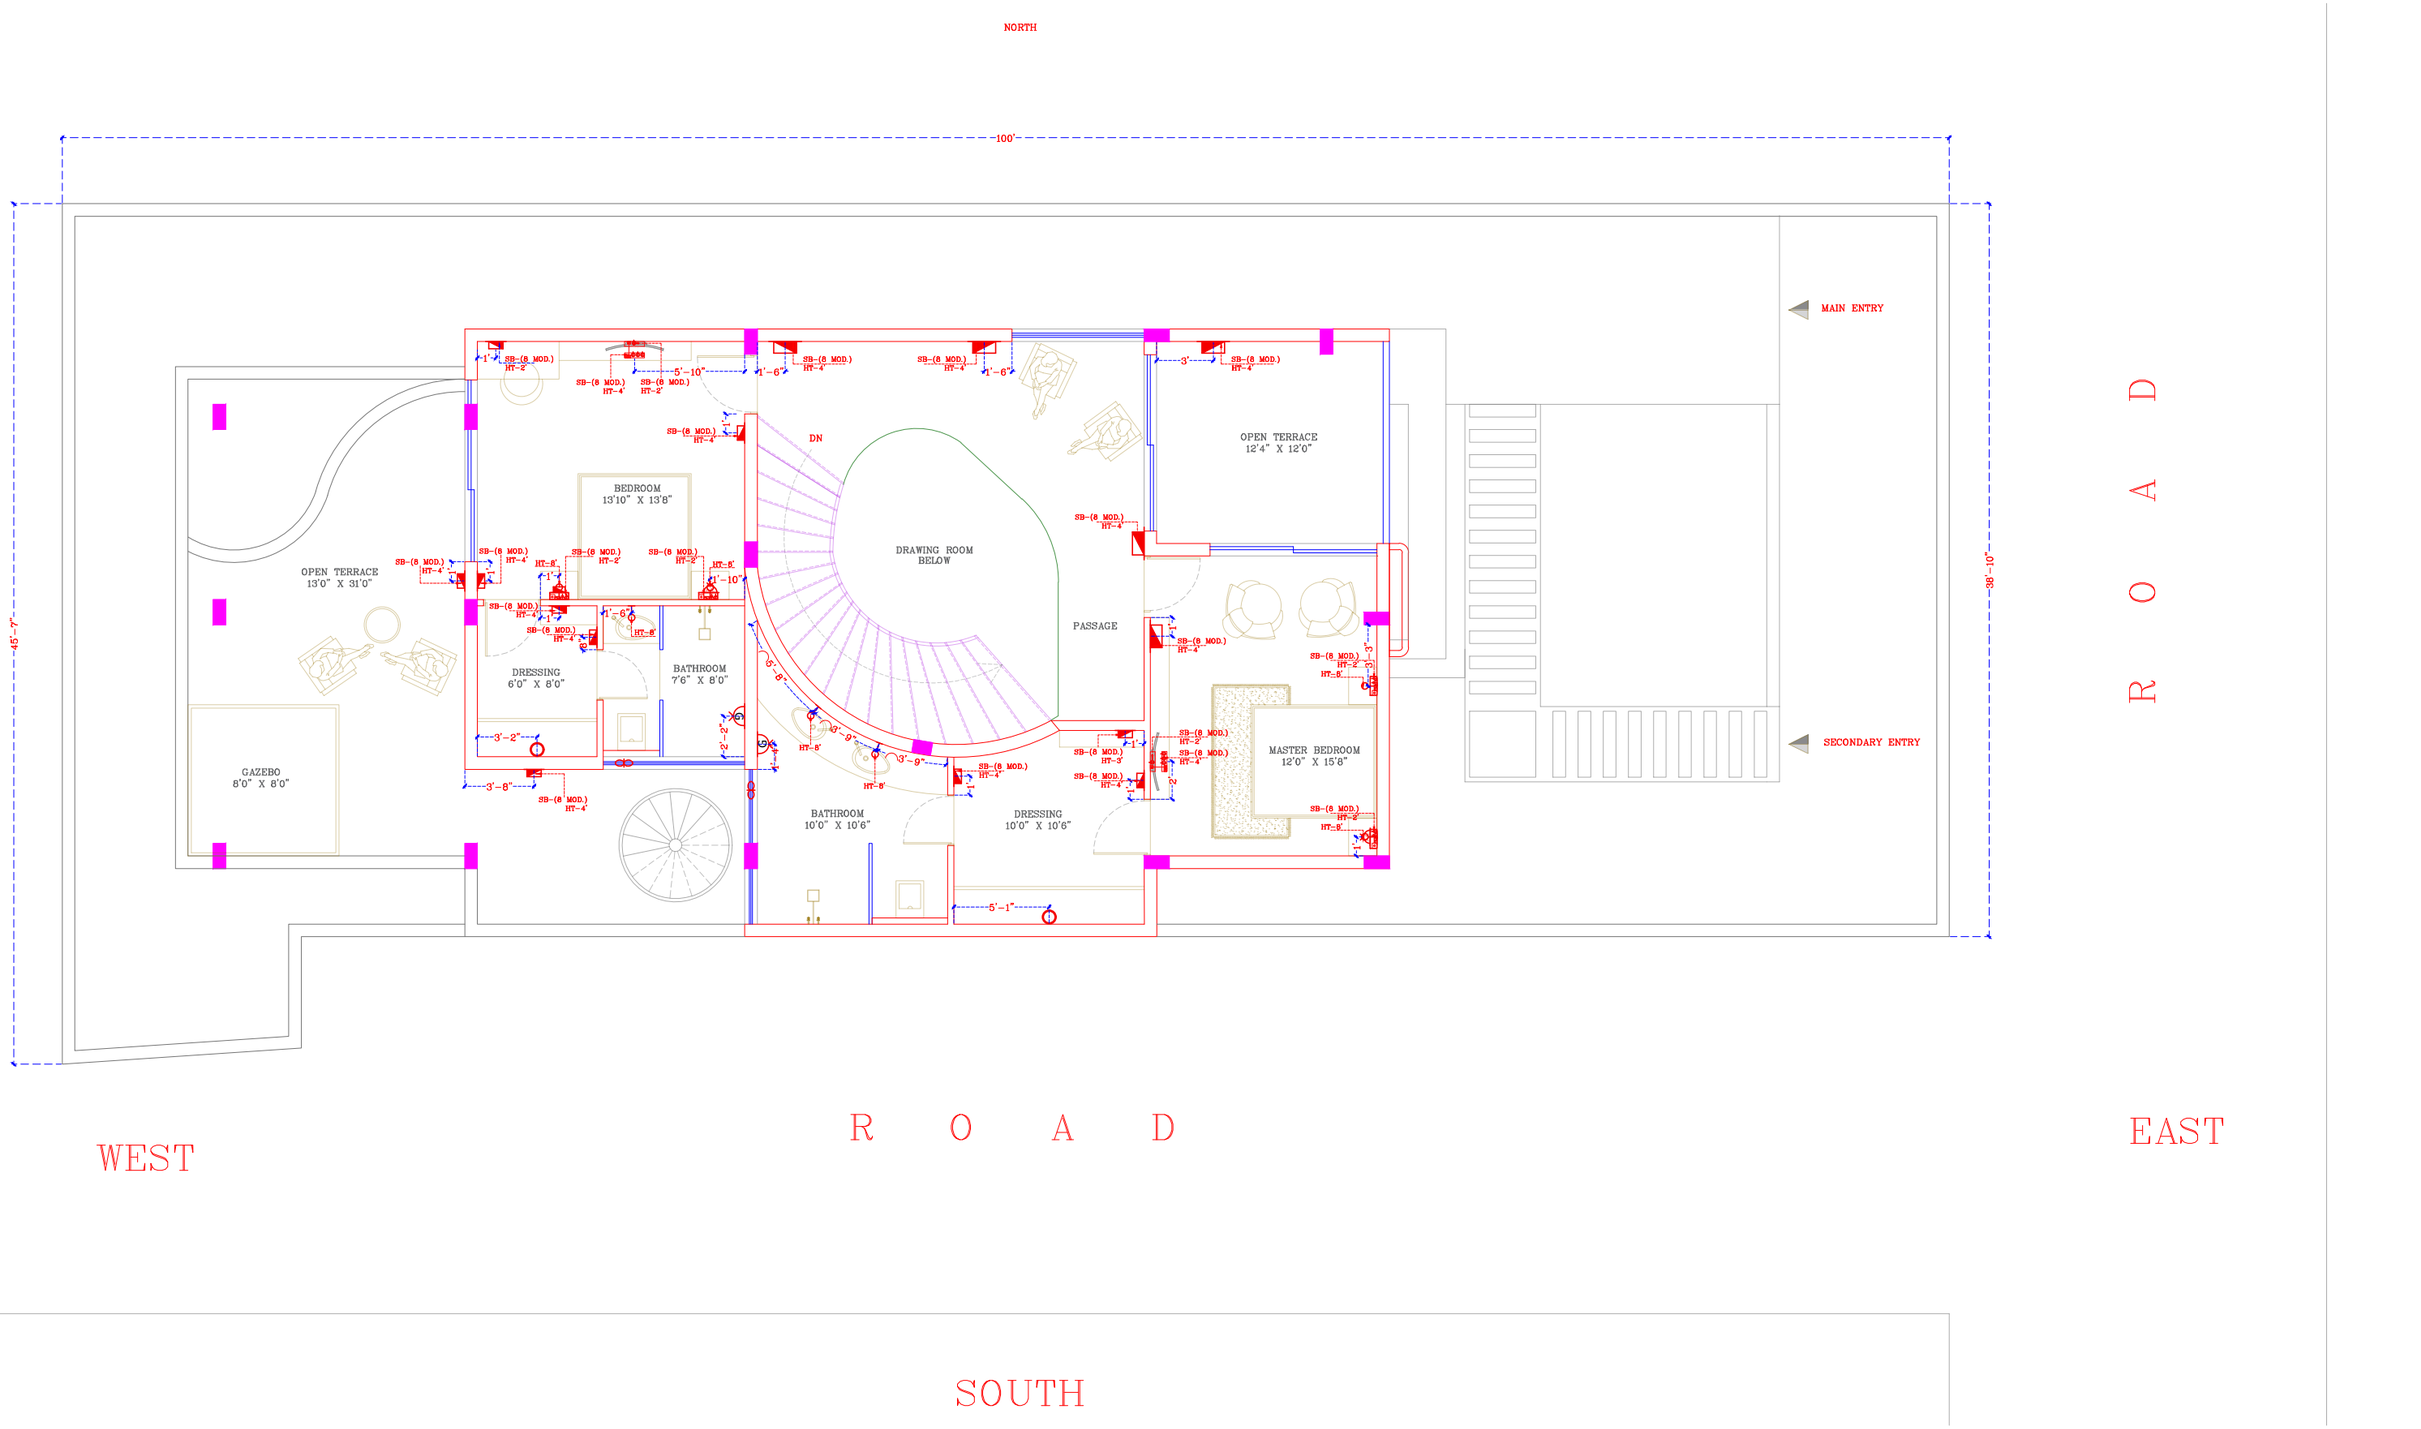

FIRST FLOOR WALL ELECTRICAL DETAIL

PROPOSED LAYOUT FOR
MR.SANJAY JI

DESIGNED BY: AR. EKTA MISHRA

A4 A R C H I T E C T

NORTH