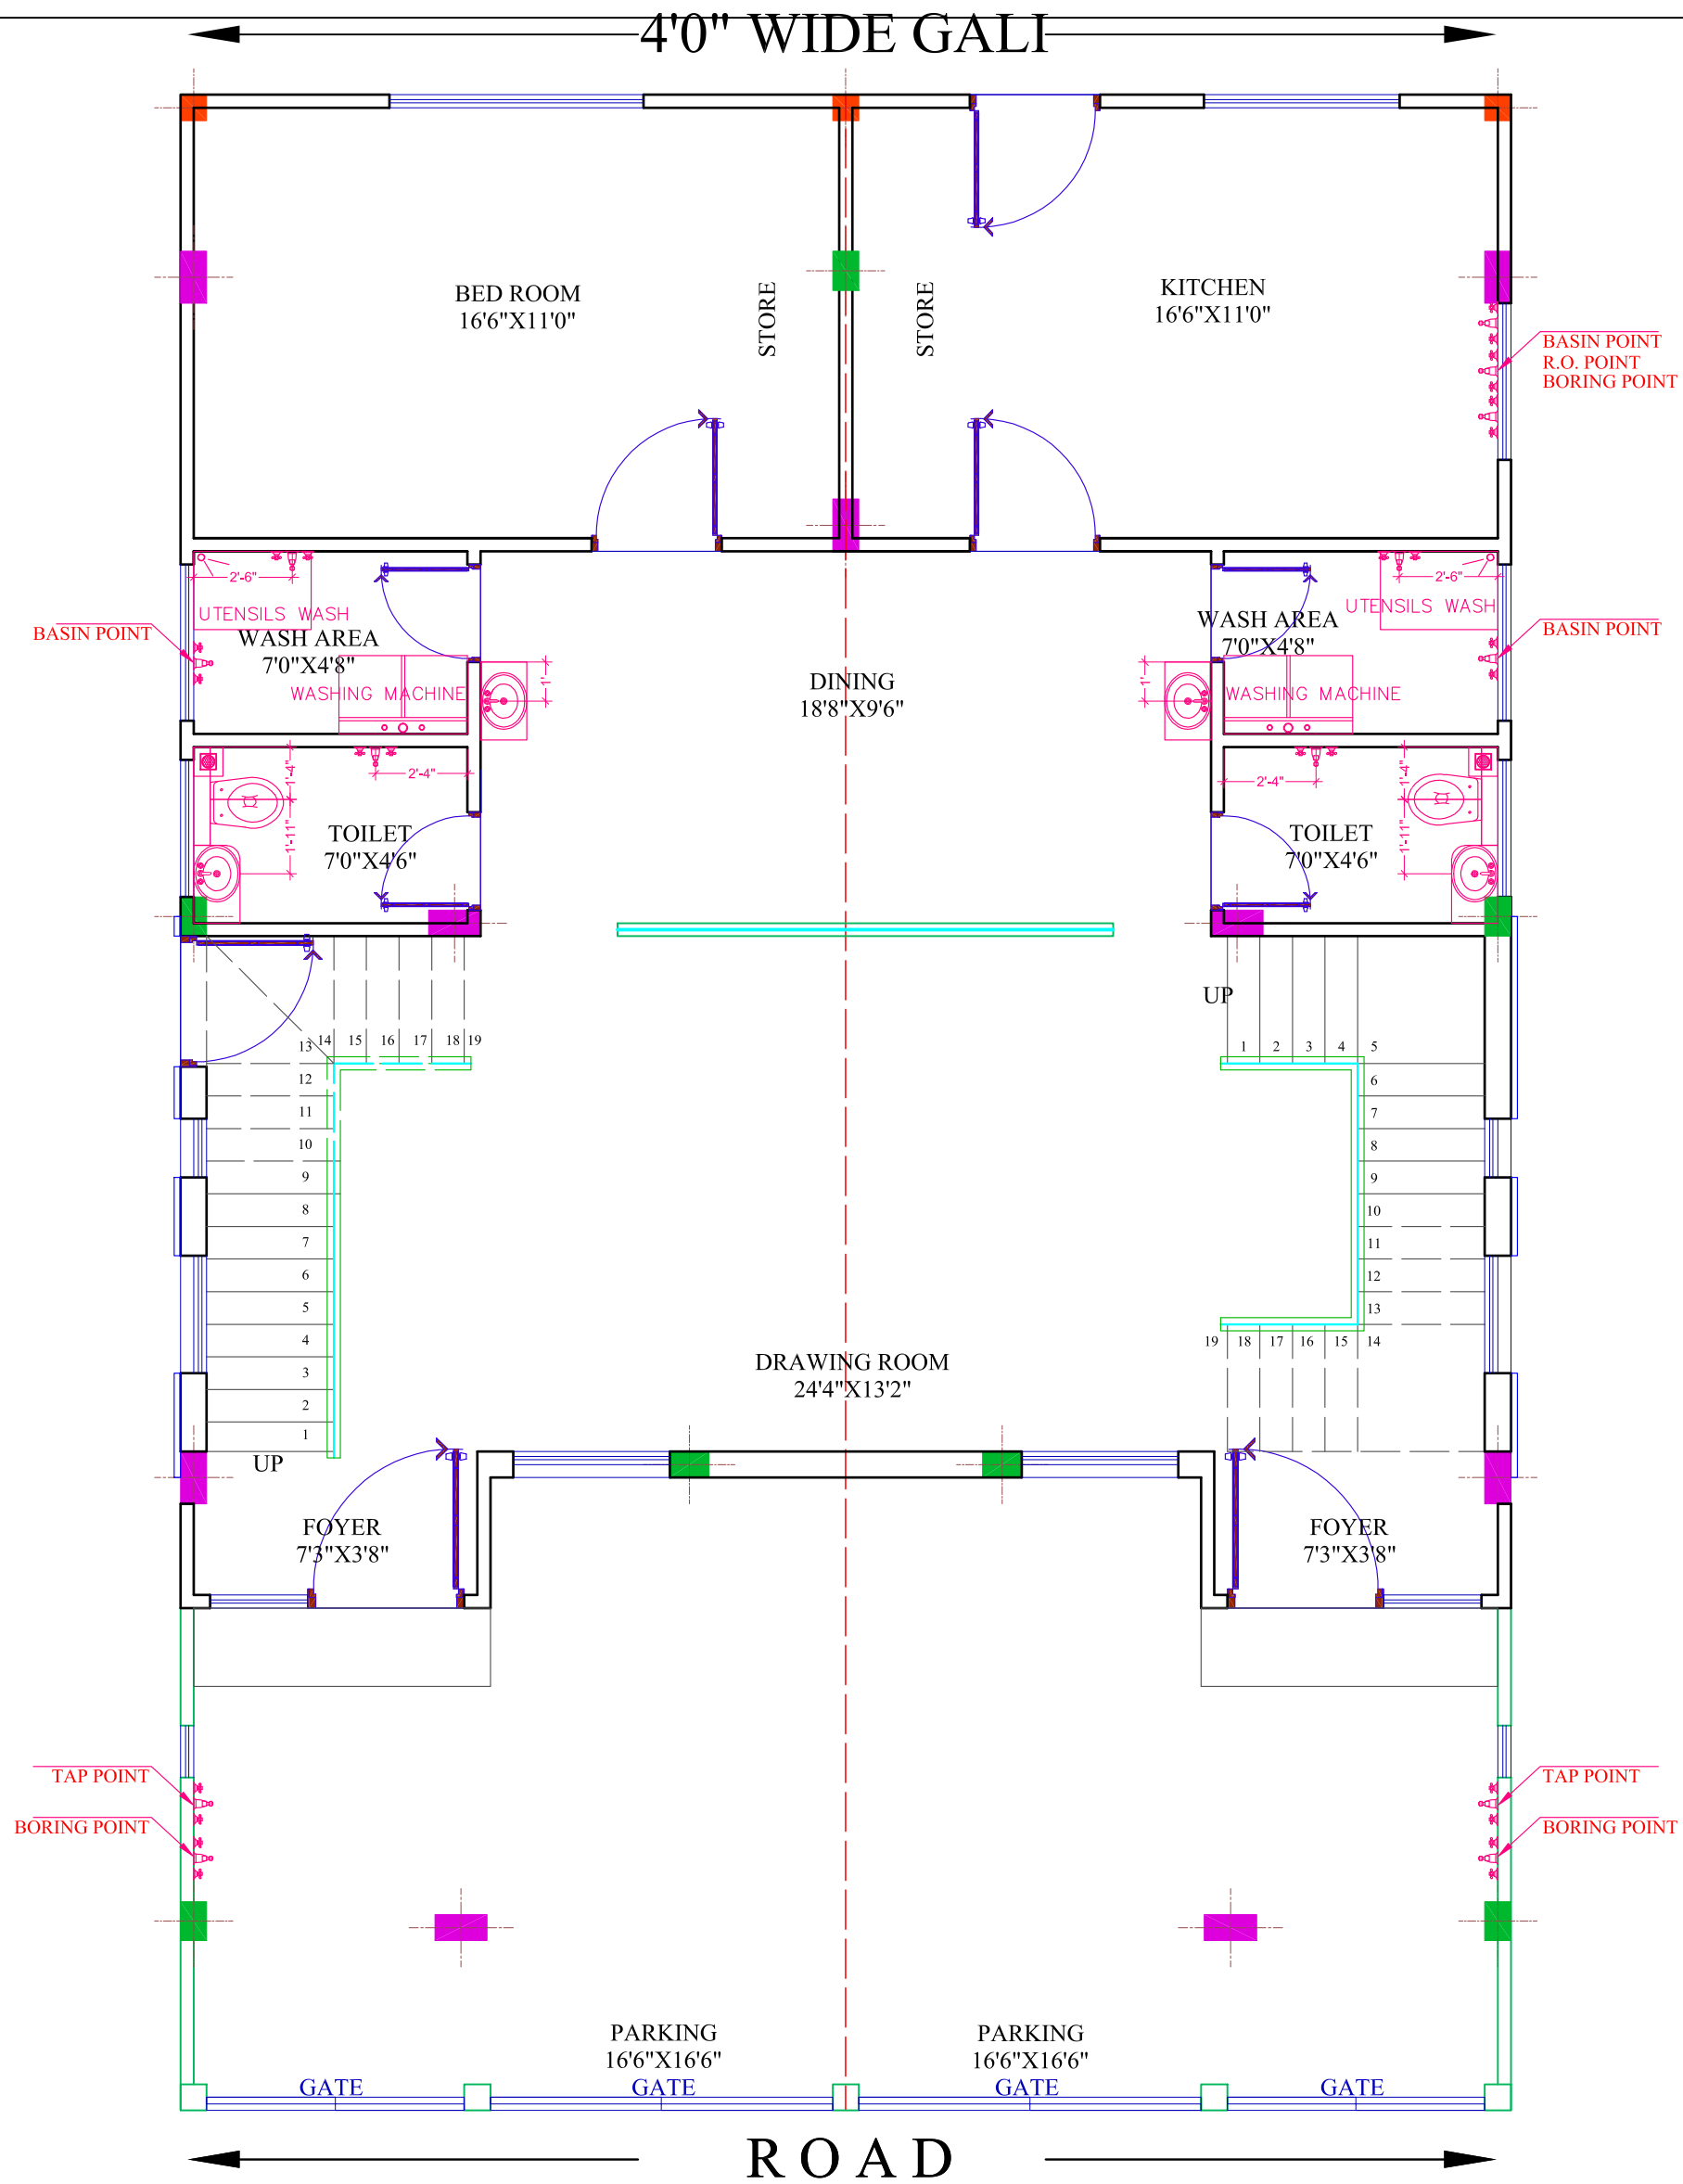


# GROUND FLOOR PLAN
# PLUMBING DETAILS

SHEET NO.13

GENERAL NOTES
1. ALL DIMENSIONS & LEVELS ARE IN FT & INCHES.
2. THIS DRAWING IS TO BE READ IN CONJUNCTION WITH THE RELEVANT ARCHITECTURAL DRAWINGS, SERVICE CONSULTANTS DRGS AND CIVIL CONTRACT DOCUMENT.
3. DO NOT SCALE THE DRAWING.
4. ANOMALIES IF ANY SHALL BE RESOLVED WITH K.AASIF & ASSOCIATES PRIOR TO EXECUTION OF WORK.
5. FOLLOW LATEST REVISION OF ALL RELEVENT DRAWINGS.
6. 'HOLD' MARK MEANS WORK SHALL NOT BE EXECUTED
7. ONLY 'VALID FOR CONSTRUCTION' DRG. SHALL BE USED FOR EXECUTION OF WORK.
8. CONTACTOR SHALL CHECK ALL DIMENSIONS AND LEVELS BEFORE EXECUTION OF WORK.

| NO. | DATE | DESCRIPTION | DRN.BY |
|---|---|---|---|
| R0 | 27/09/2024 | FOR PROPOSAL | AASIF |

REVISIONS

CLIENT: Mr. RAHUL JIJA

PROJECT: RESIDENTIAL BUILDING AT DEWAS

DRG. TITLE: SANATRY PLAN

| DRN. BY | CHD. BY | APPR. BY | PROJECT NO. | DRG.NO. | REV. NO. |
|---|---|---|---|---|---|
| AASIF KHAN | A.K | A.K | 120624 | 120624/A-01 | R0 |

THIS DRAWING IS THE SOLE PROPERTY OF K.Aasif & ASSOCIATES

E:\k.aasif and associates\client records\2024 projects\er ajay sir\rahul jija ajay sir\new folder\0000 all drawings 12 3 2024.dwg

ENGINEER,ARCHITECT & Project Consultant
K.AASIF & ASSOCIATES
ER. AASIF KHAN
M.TECH STRUCTURE
PH.NO.: +91-8720003869
E-Mail : aasif.khan0047@gmail.com