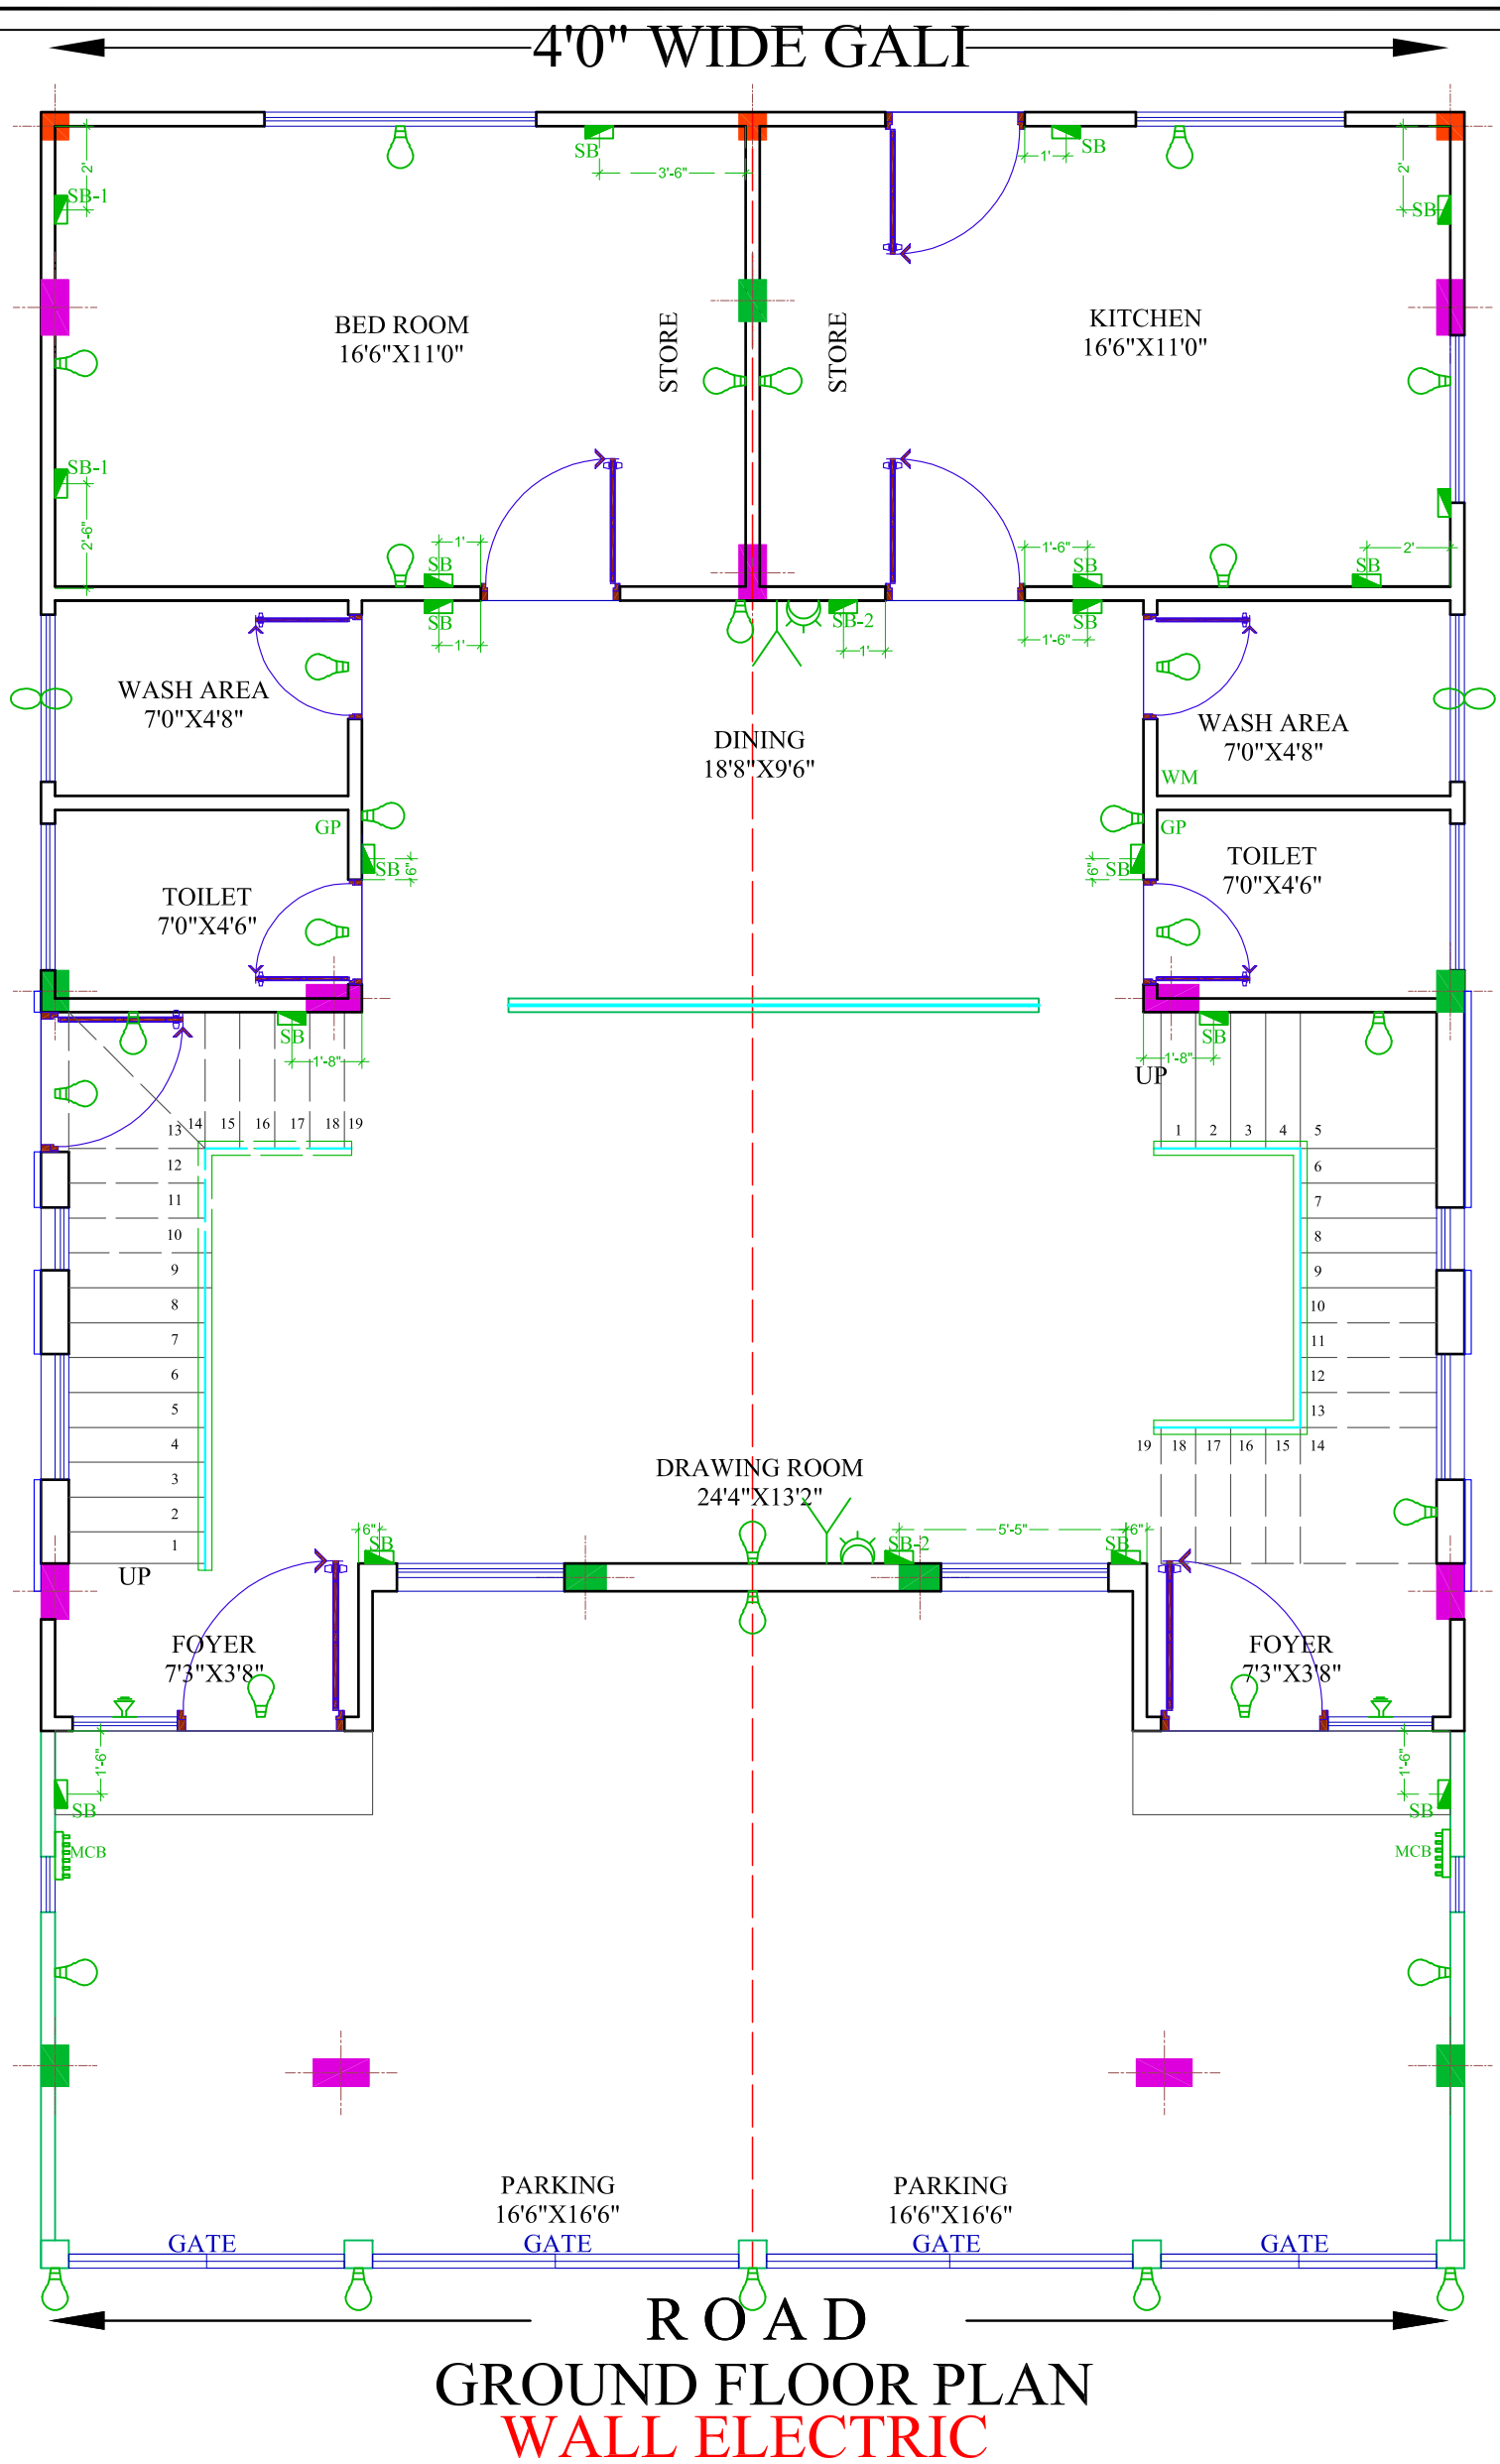

GROUND FLOOR PLAN
WALL ELECTRIC

WALL LIGHT POINT	
TELEVISION ENTENA (HT+36")	
TELEPHONE POINT(22")	
EXHAUST FAN	
15 AMP POWER POINT	
SWITCH BOARD (HT.=54") ALL POINTS SWITCH & 5 AMP POWER POINT	SB
5 AMP POWER POINT	
BELL SWITCH POINT	
BELL LOCATION POINT	
MAIN CIRCUIT BOARD	MCB
GYSER POINT	GP
WASHING MACHINE	WM
TWO WAY SWITCH , (HT-22" TELEPHONE POINT & 5 AMP POWER POINT	SB -1
T.V. POINT & (HT-36") 15 AMP POWER POINT	SB -2

SHEET NO.13

GENERAL NOTES
1. ALL DIMENSIONS & LEVELS ARE IN FT & INCHES.
2. THIS DRAWING IS TO BE READ IN CONJUNCTION WITH THE RELEVANT ARCHITECTURAL DRAWINGS, SERVICE CONSULTANTS DRGS AND CIVIL CONTRACT DOCUMENT.
3. DO NOT SCALE THE DRAWING.
4. ANOMALIES IF ANY SHALL BE RESOLVED WITH K.AASIF & ASSOCIATES PRIOR TO EXECUTION OF WORK.
5. FOLLOW LATEST REVISION OF ALL RELEVENT DRAWINGS.
6. 'HOLD' MARK MEANS WORK SHALL NOT BE EXECUTED
7. ONLY 'VALID FOR CONSTRUCTION' DRG. SHALL BE USED FOR EXECUTION OF WORK.
8. CONTACTOR SHALL CHECK ALL DIMENSIONS AND LEVELS BEFORE EXECUTION OF WORK.

NO.	DATE	DESCRIPTION	DRN.BY
R0	27/08/2020	FOR PROPOSAL	AASIF

REVISIONS

CLIENT: Mr. RAHUL JIJA

PROJECT: RESIDENTIAL BUILDING AT DEWAS

DRG. TITLE: WALL ELECTRIC

DRN. BY	CHD. BY	APPR. BY	PROJECT NO.	DRG.NO.	REV. NO.
AASIF KHAN	A.K	A.K	120624	120624/A-01	R0

THIS DRAWING IS THE SOLE PROPERTY OF K.Aasif & ASSOCIATES

E:\k.aasif and associates\client records\2024 projects\er ajay sir\rahul jija ajay sir\new folder\0000 all drawings 12 3 2024.dwg

ENGINEER,ARCHITECT & Project Consultant
K.AASIF & ASSOCIATES
ER. AASIF KHAN
M.TECH STRUCTURE
PH.NO.: +91-8720003869
E-Mail : aasif.khan0047@gmail.com